FAMILY COMPOUND

Chott Meriem - SOUSSE

Architectes: Marwen MTIMET
Anis BOUDEN

AMÉNAGEMENT GÉNÉRAL

Démarche

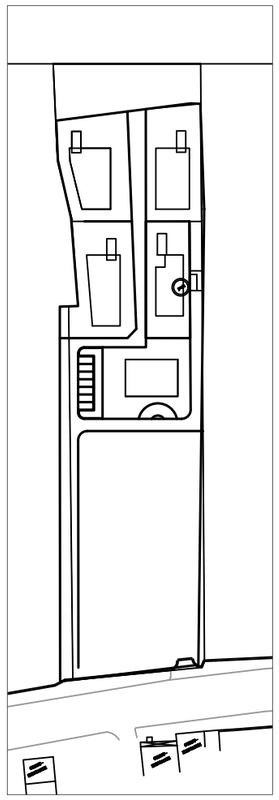

Variante 1

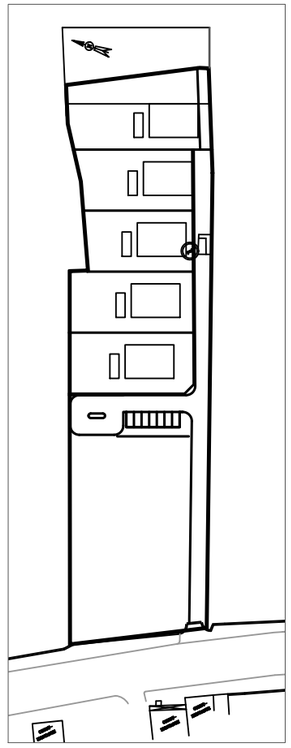

Variante 2

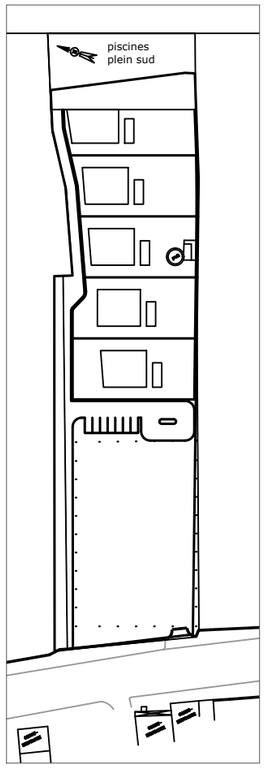

Variante 3

Variante 4 retenue

FAMILY COMPOUND

Chott Meriem - SOUSSE

Architectes: Marwen MTIMET
Anis BOUDEN

AMÉNAGEMENT GÉNÉRAL

Démarche

Variante 4 retenue

- La variante 4 est la plus adaptée à la forme du terrain tout en maintenant une certaine équité entre les lots.
- Cette disposition assure aux maisons une bonne orientation et une vue mer depuis les salons, terrasses et suites.
- Un espace central aménagé en jardin est au coeur du compound, cet espace anime le projet, permet au maisons d'avoir assez de retrait les unes par rapport aux autres et assez de recul pour avoir une vue mer.
- Un circuit piéton aménagé en esplanade verdoyante longe le projet depuis le parking jusqu'à la plage, ce circuit dessert notamment les maisons et l'espace commun aménagé en jardin.
- Un circuit véhiculer de 6 mètres de largeur dessert tous les lots, un parking de 11 places est aménagé.

Genèse d'un compound vivant et animé.

FAMILY COMPOUND

Chott Meriem - SOUSSE

Architectes: Marwen MTIMET
Anis BOUDEN

AMBIANCE GÉNÉRALE

Perspectives

Vues Séquentielles sur le circuit Piéton

FAMILY COMPOUND

Chott Meriem - SOUSSE

Architectes: Marwen MTIMET
Anis BOUDEN

AMBIANCE GÉNÉRALE

Perspectives

Architecture Contemporaine

Une architecture qui tend à privilégier le confort de vie optimisé et le bien être.
Cadre Verdoyant, Formes Sobres, Lignes Pures.
Maisons économiques en énergie, dotées d'espaces de vie spacieux et de lignes design, maisons ouvertes sur la nature

Vues Séquentielles sur le circuit Piéton

FAMILY COMPOUND

Chott Meriem - SOUSSE

Architectes: Marwen MTIMET
Anis BOUDEN

Jardin Commun

- Un jardin commun au coeur du compound anime le projet, permet au maisons d'avoir assez de retrait les unes par rapport aux autres et assez de recul pour avoir une vue mer.
- Le jardin est conçu principalement autour de l'élément végétal et l'élément aquatique.
- L'eau apparaît, sous forme de jets d'eau, de cascades et de fontaines.
- Un salon extérieur convivial encaissé dans le plan d'eau autour d'une cheminée.
- éclairage extérieur sophistiqué, projections sur les façades et interactif avec les usagers de l'espace.

Le but visé par cette architecture contemporaine
est de rendre le compound plus vivant et plus animé.

FAMILY COMPOUND

Chott Meriem - SOUSSE

Architectes: Marwen MTIMET
Anis BOUDEN

Jardin Commun

FAMILY COMPOUND

Chott Meriem - SOUSSE

Architectes: Marwen MTIMET
Anis BOUDEN

FAMILY COMPOUND

Chott Meriem - SOUSSE

Villa 1	
Surface terrain	808 m²
Surface RDC	270 m²
Surface Etage	294,5 m²
Surface totale Couverte	564,5 m²

Villa 2	
Surface terrain	694,5 m²
Surface RDC	257,5 m²
Surface Etage	270 m²
Surface totale Couverte	527,5 m²

Villa 3	
Surface terrain	700 m²
Surface RDC	268,1 m²
Surface Etage	253,6 m²
Surface totale Couverte	521,7 m²

Villa 4	
Surface terrain	759,6 m²
Surface RDC	247,3 m²
Surface Etage	266,5 m²
Surface totale Couverte	513,8 m²

Villa 5	
Surface terrain	703,4 m²
Surface RDC	221 m²
Surface Etage	225,2 m²
Surface totale Couverte	446,2 m²

terrasse plage non constructible	1000 m²
jardin commun	472 m²
locaux annexes	83 m²
Réserve foncière	1037 m²
piscine couverte (extensible)	242 m²

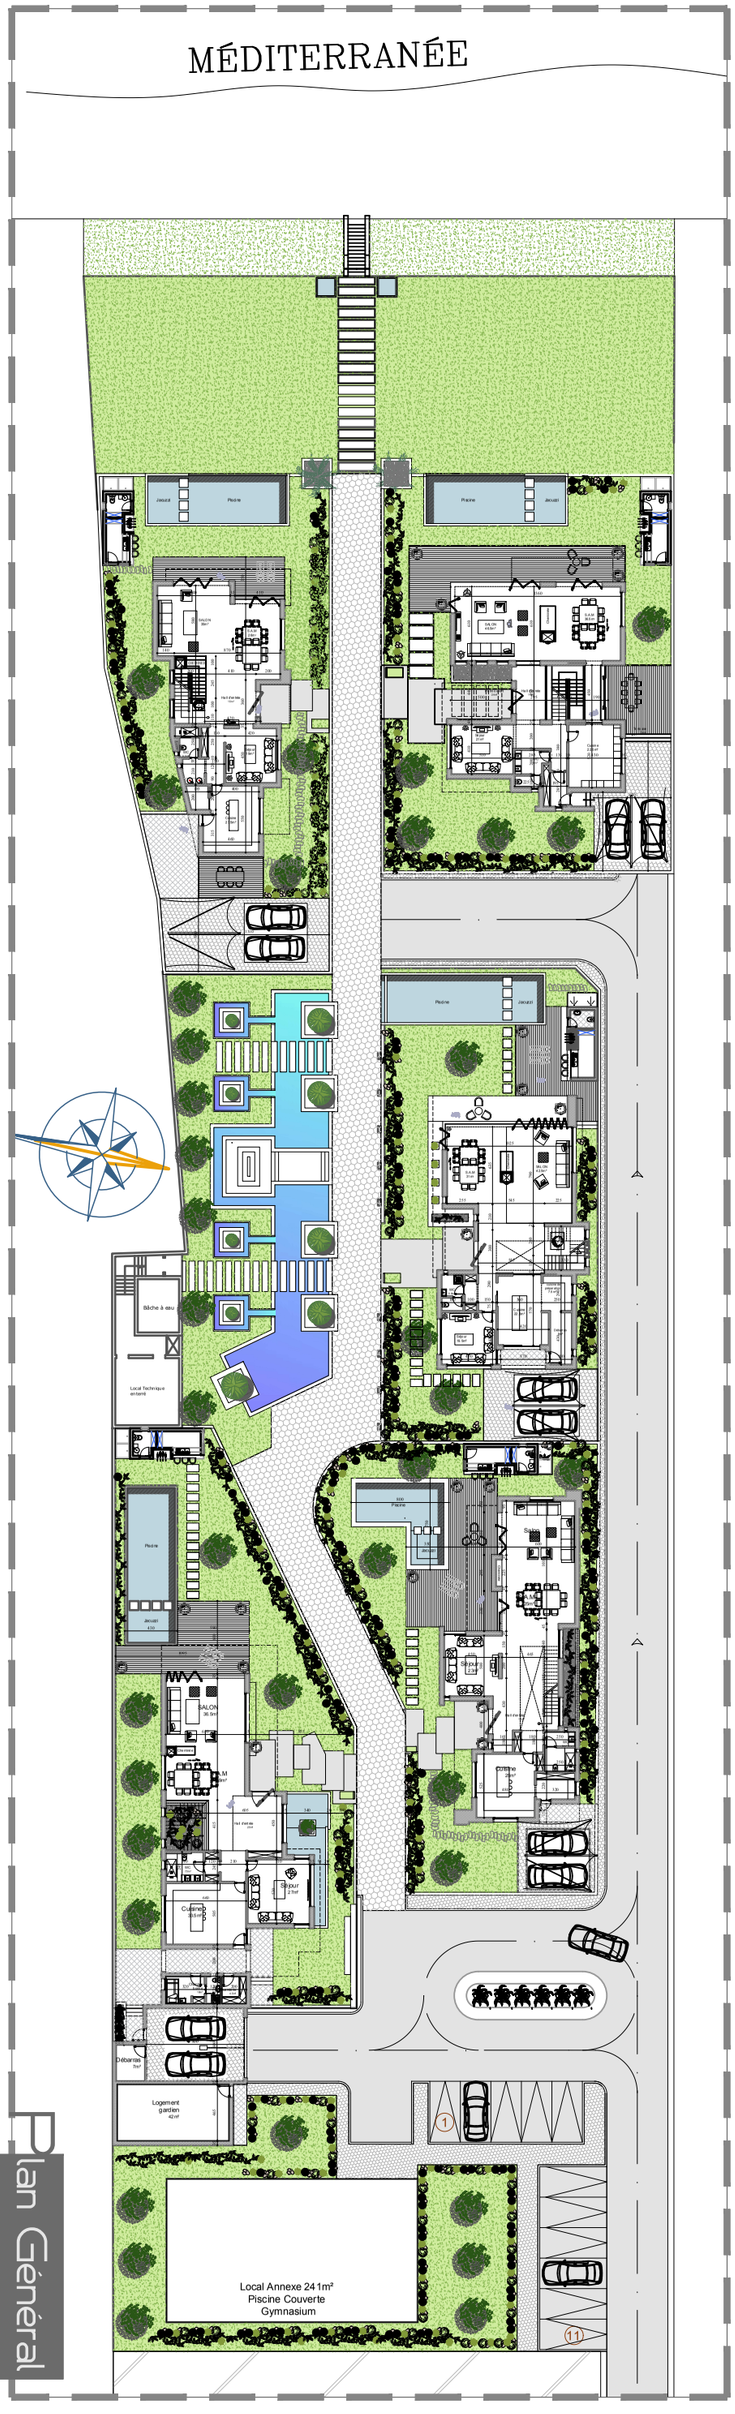

Plan Général

AMBIANCE GÉNÉRALE

Perspectives

Architectes: Marwen MTIMET
Anis BOUDEN

AMBIANCE GÉNÉRALE

Perspectives

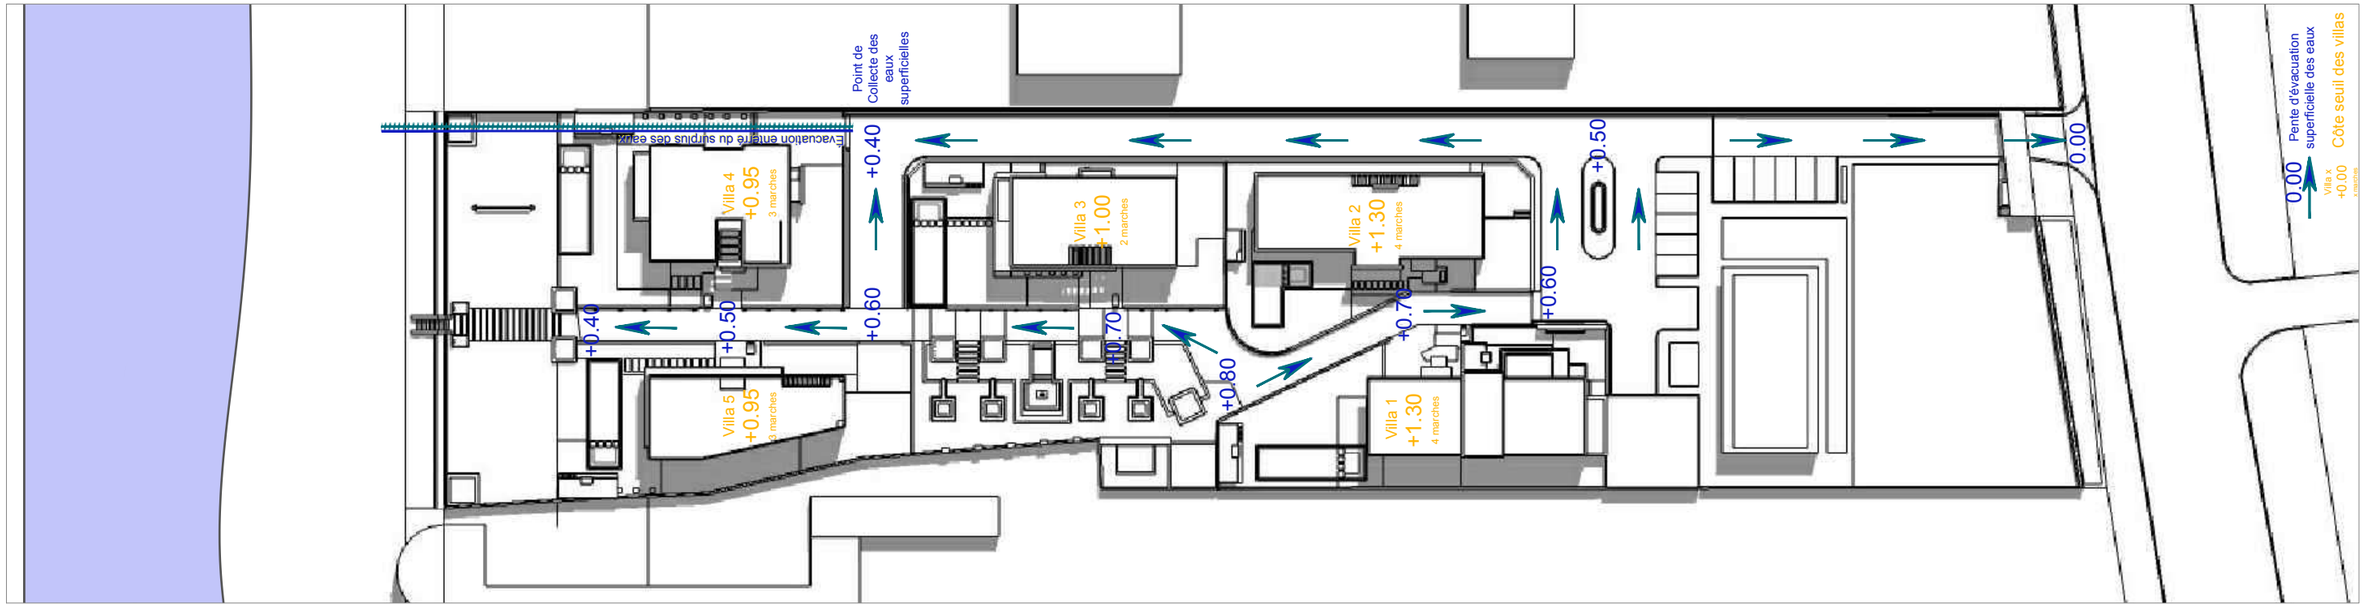

Plan d'évacution des eaux et cotes maisons

Matériaux Novateurs

Verre Bois Marbre Aluminium Inox Galets

Noblesse et Efficacité énergétique

FAMILY COMPOUND

Chott Meriem - SOUSSE

Architectes: Marwen MTIMET
Anis BOUDEN

Villa

FAMILY COMPOUND

Chott Meriem - SOUSSE

Architectes: Marwen MTIMET
Anis BOUDEN

Villa 1

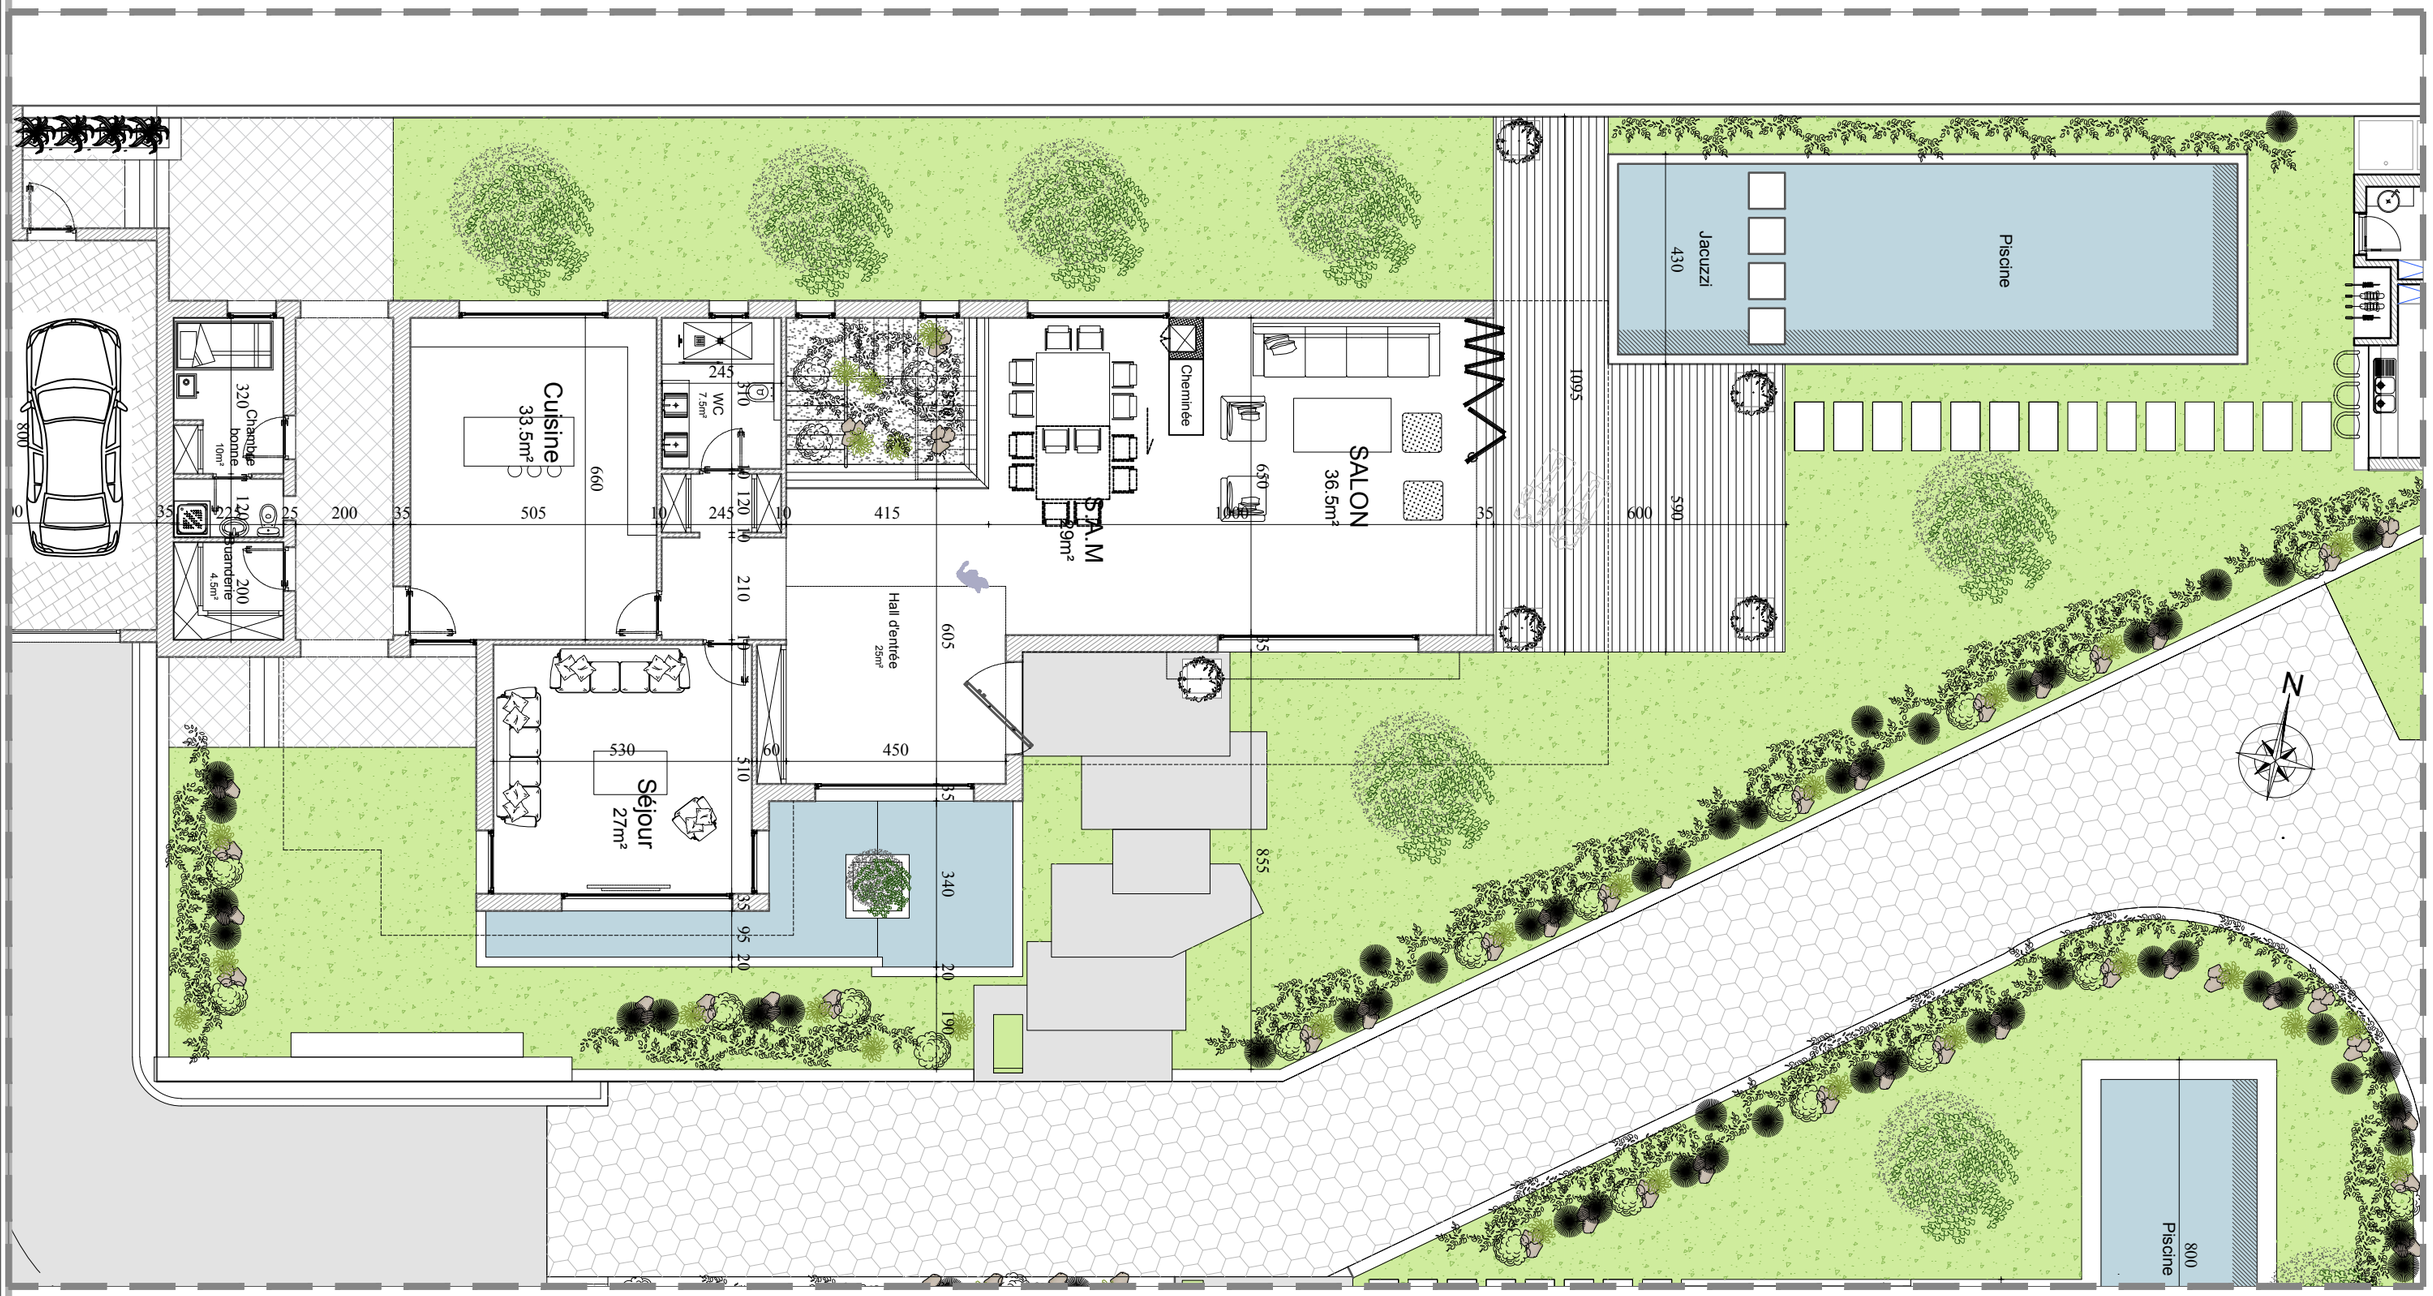

Plan Rez De Chaussée

Echelle 1/25

FAMILY COMPOUND

Chott Meriem - SOUSSE

Architectes: Marwen MTIMET
Anis BOUDEN

Villa 1

Situation Repérage

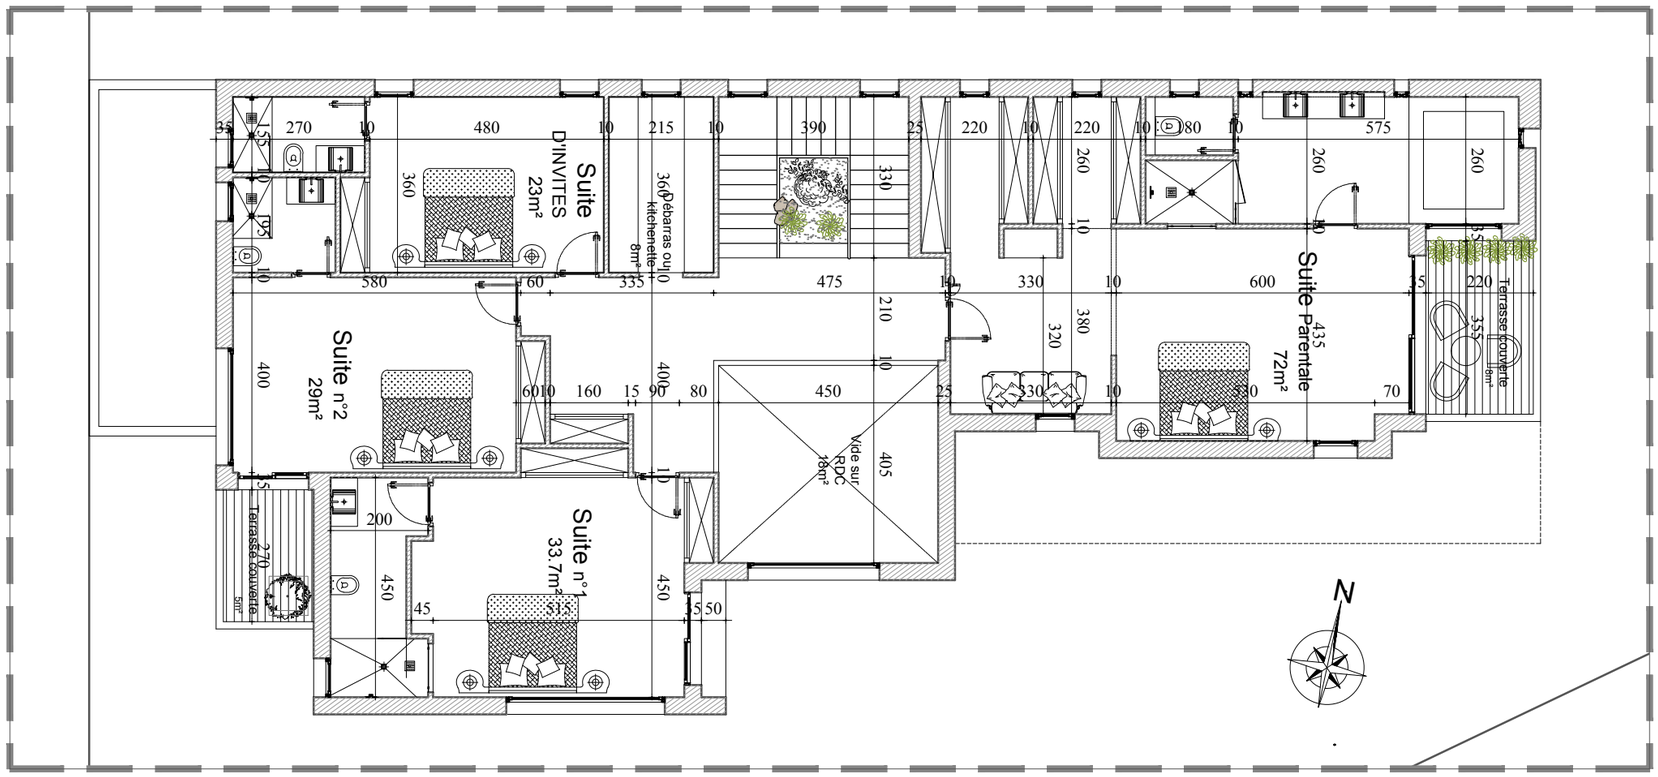

Plan Étage

Echelle 1/50

Villa 1	
Surface terrain	808 m²
Surface RDC	270 m²
Surface Etage	294,5 m²
Surface totale couverte	564,5 m²

Family Compound

Chott Meriem - Sousse

Architectes: Marwen MTIMET
Anis BOUDEN

Villa 1

FAMILY COMPOUND

Chott Meriem - SOUSSE

Architectes: Marwen MTIMET
Anis BOUDEN

Villa 1

FAMILY COMPOUND

Chott Meriem - SOUSSE

Architectes: Marwen MTIMET
Anis BOUDEN

Villa

FAMILY COMPOUND

Chott Meriem - SOUSSE

Architectes: Marwen MTIMET
Anis BOUDEN

Villa 2

N

Piscine
800
Jacuzzi
350
750

Séjour
23m²
450
500
400

Cuisine
25m²
480
525

Hall d'entrée
10m²

S.A.M
25m²

Salon
30m²
600

Cheminée

WC
8m²

330 295 350 130
400
35 350 35 225 35 350 95
1010
150 220 195 120 35 240 315 240 45
320
250
250
70
180
180
60
165
180 430 200 150 35
465
20 190 20 5

Plan Rez De Chaussée

Echelle 1/100

FAMILY COMPOUND

Chott Meriem - SOUSSE

Architectes: Marwen MTIMET
Anis BOUDEN

Villa 2

Situation Repérage

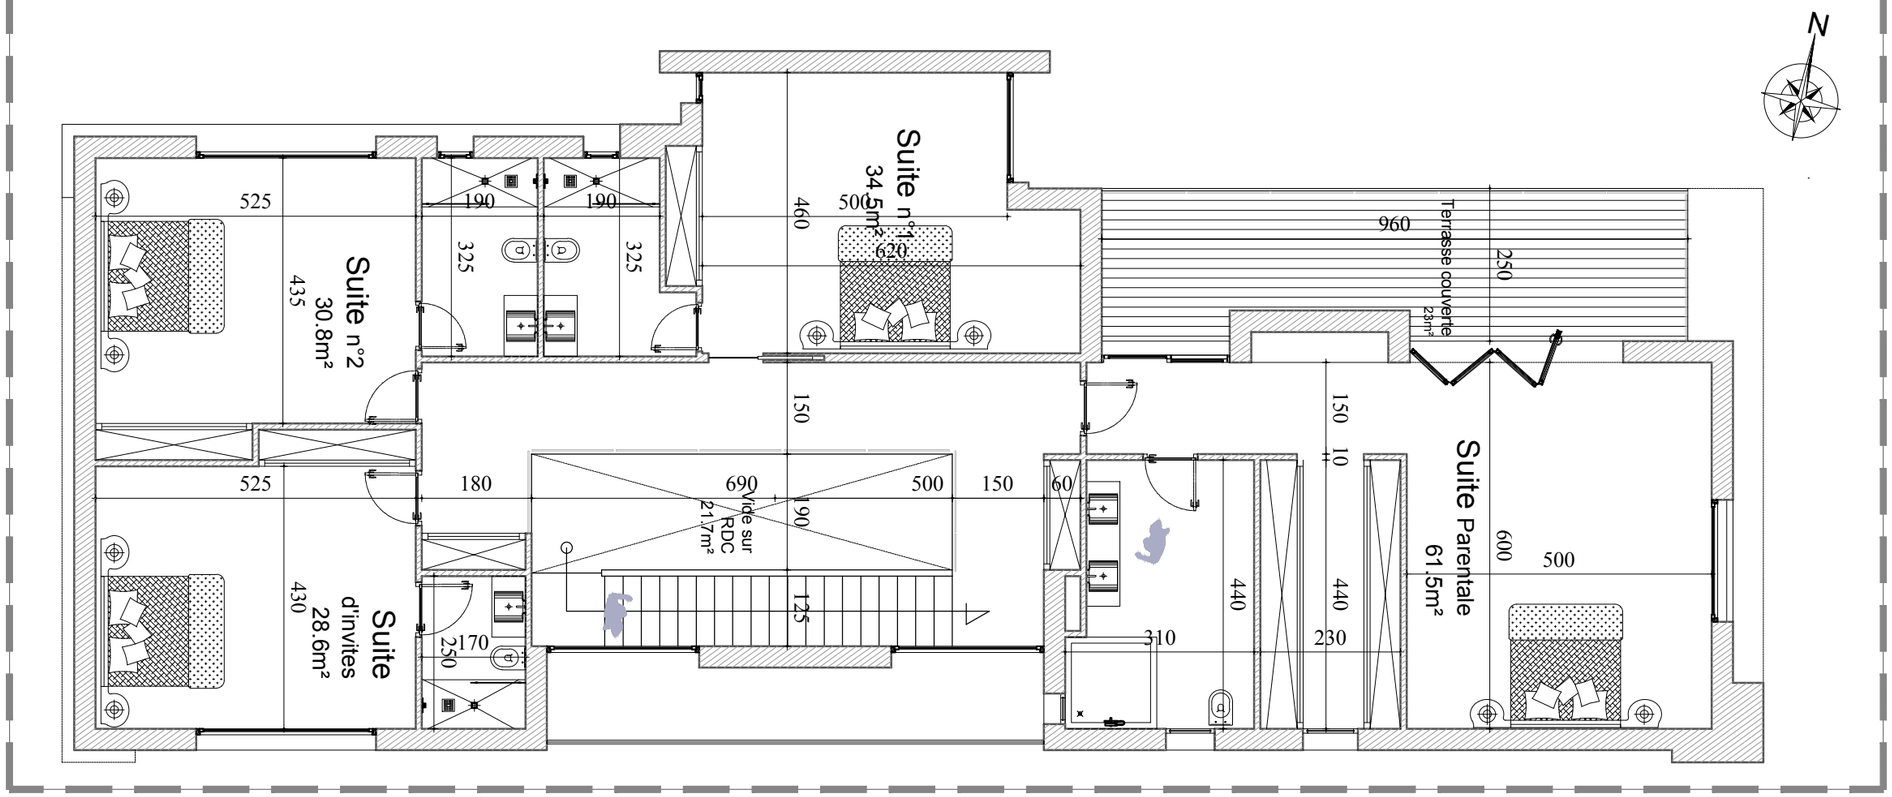

Plan Étage
Echelle 1/100

Villa 2	
Surface terrain	694,5 m²
Surface RDC	257,5 m²
Surface Etage	270 m²
Surface totale Couverte	527,5 m²

FAMILY COMPOUND

Chott Meriem - SOUSSE

Architectes: Marwen MTIMET
Anis BOUDEN

Villa 2

FAMILY COMPOUND

Chott Meriem - SOUSSE

Architectes: Marwen MTIMET
Anis BOUDEN

Villa 2

FAMILY COMPOUND

Chott Meriem - SOUSSE

Architectes: Marwen MTIMET
Anis BOUDEN

Villa 2

FAMILY COMPOUND

Chott Meriem - SOUSSE

Architectes: Marwen MTIMET
Anis BOUDEN

Villa

FAMILY COMPOUND

Chott Meriem - SOUSSE

Architectes: Marwen MTIMET
Anis BOUDEN

N

Villa 3

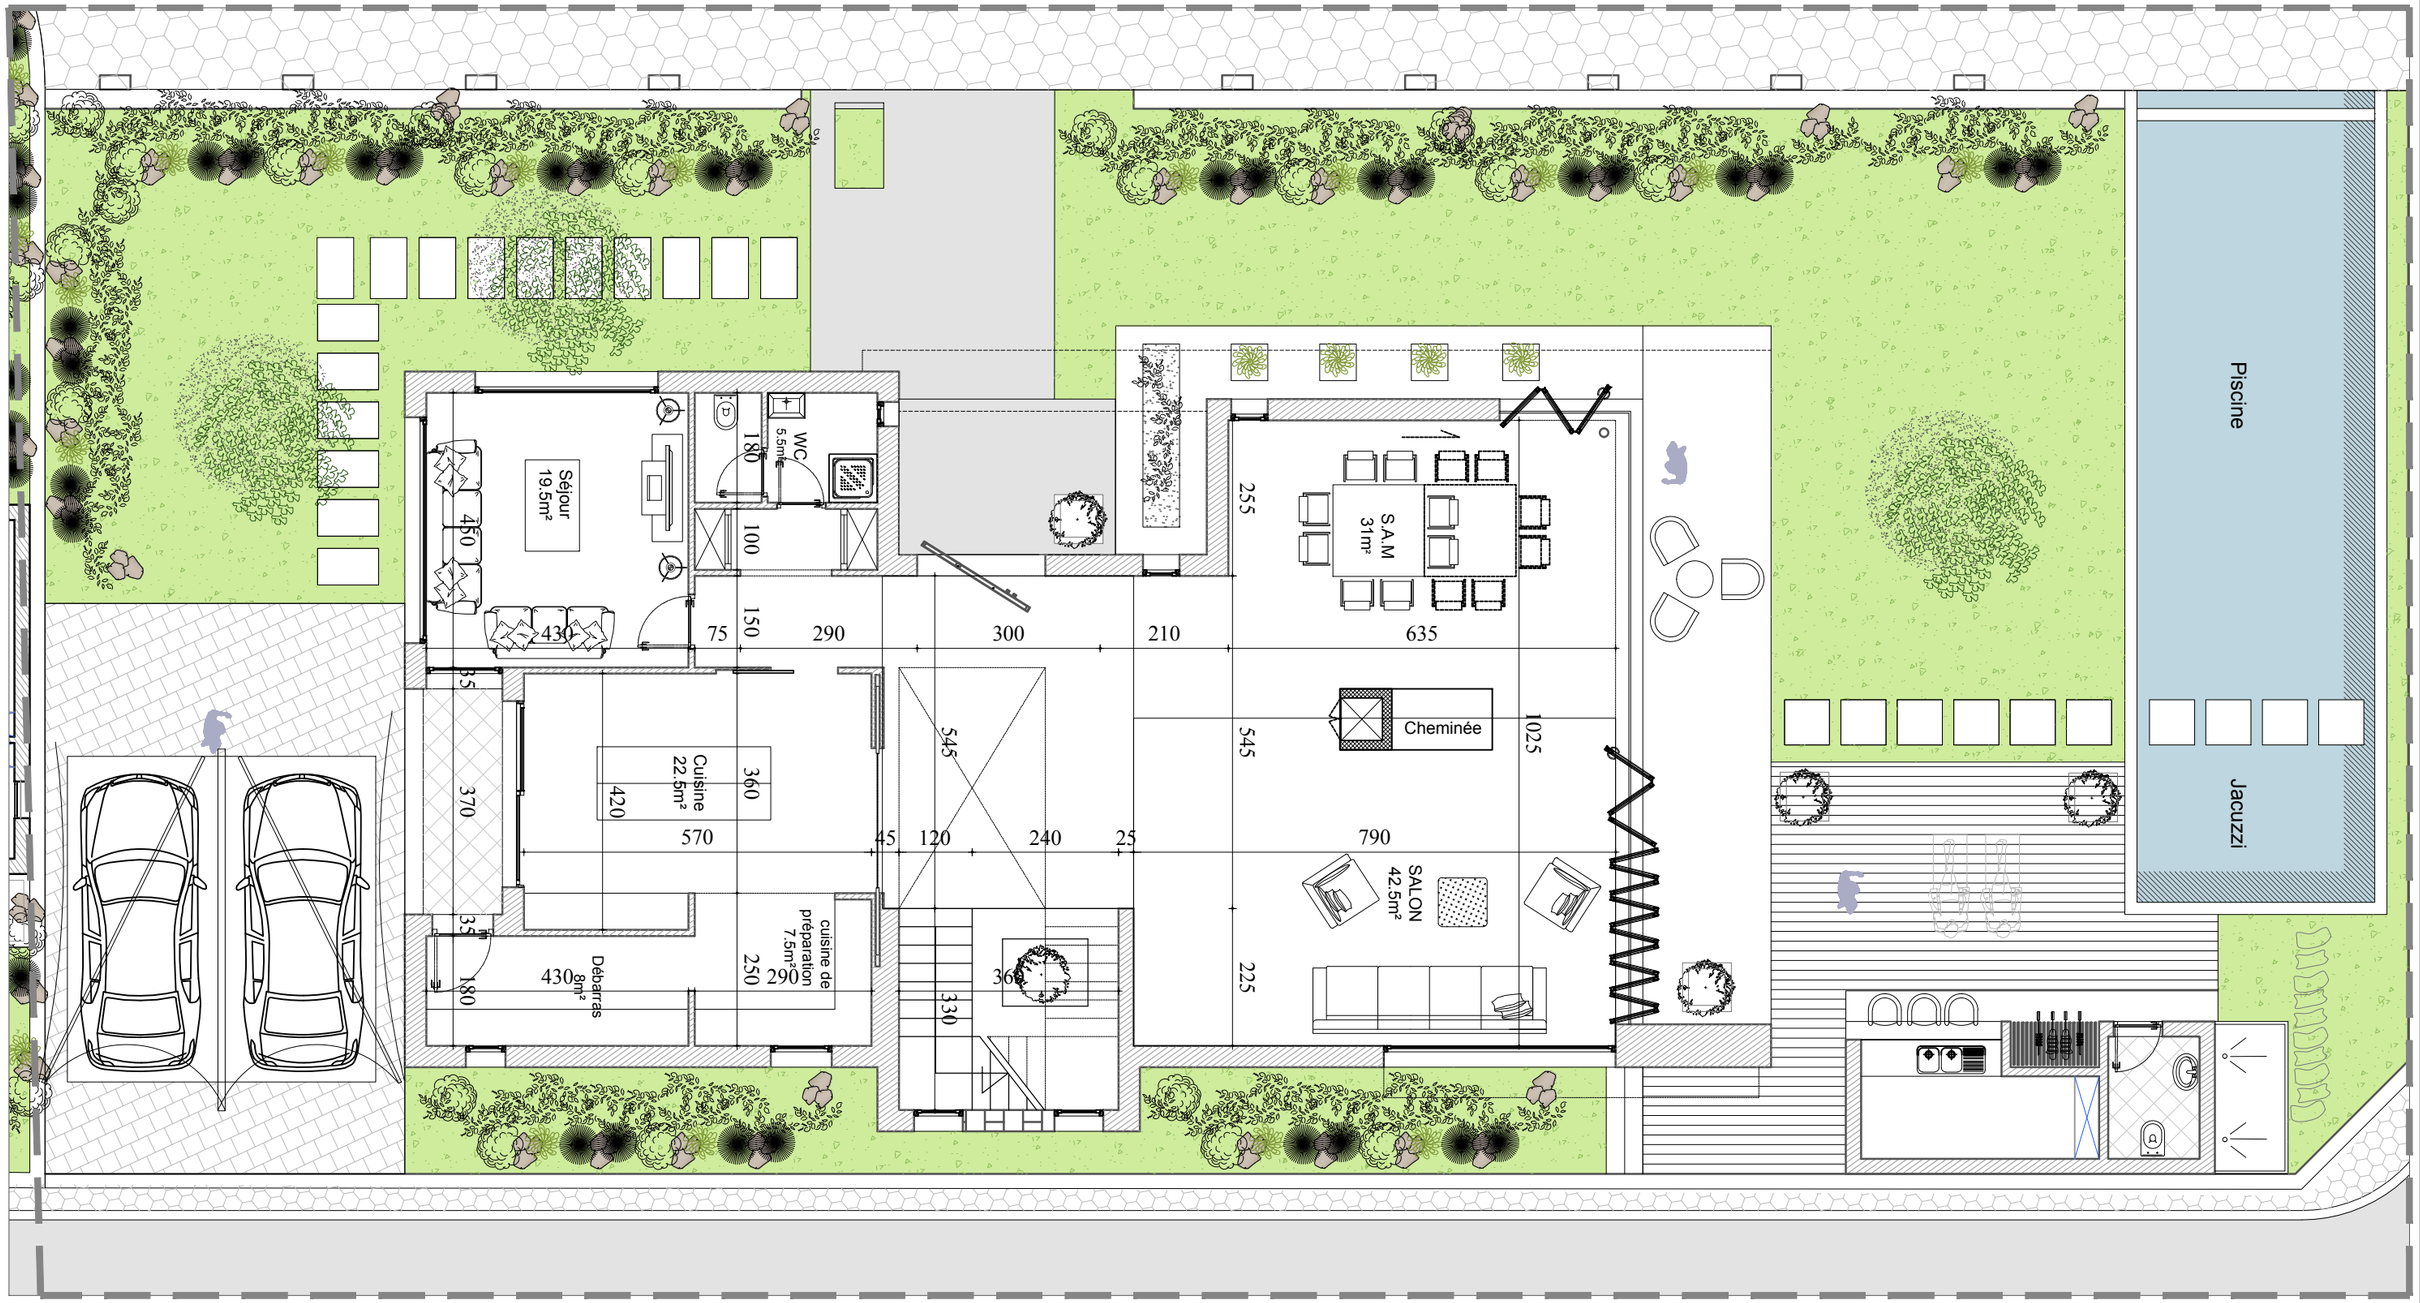

Plan Rez De Chaussée

Echelle 1/100

FAMILY COMPOUND

Chott Meriem - SOUSSE

Architectes: Marwen MTIMET
Anis BOUDEN

Villa 3

Situation Repérage

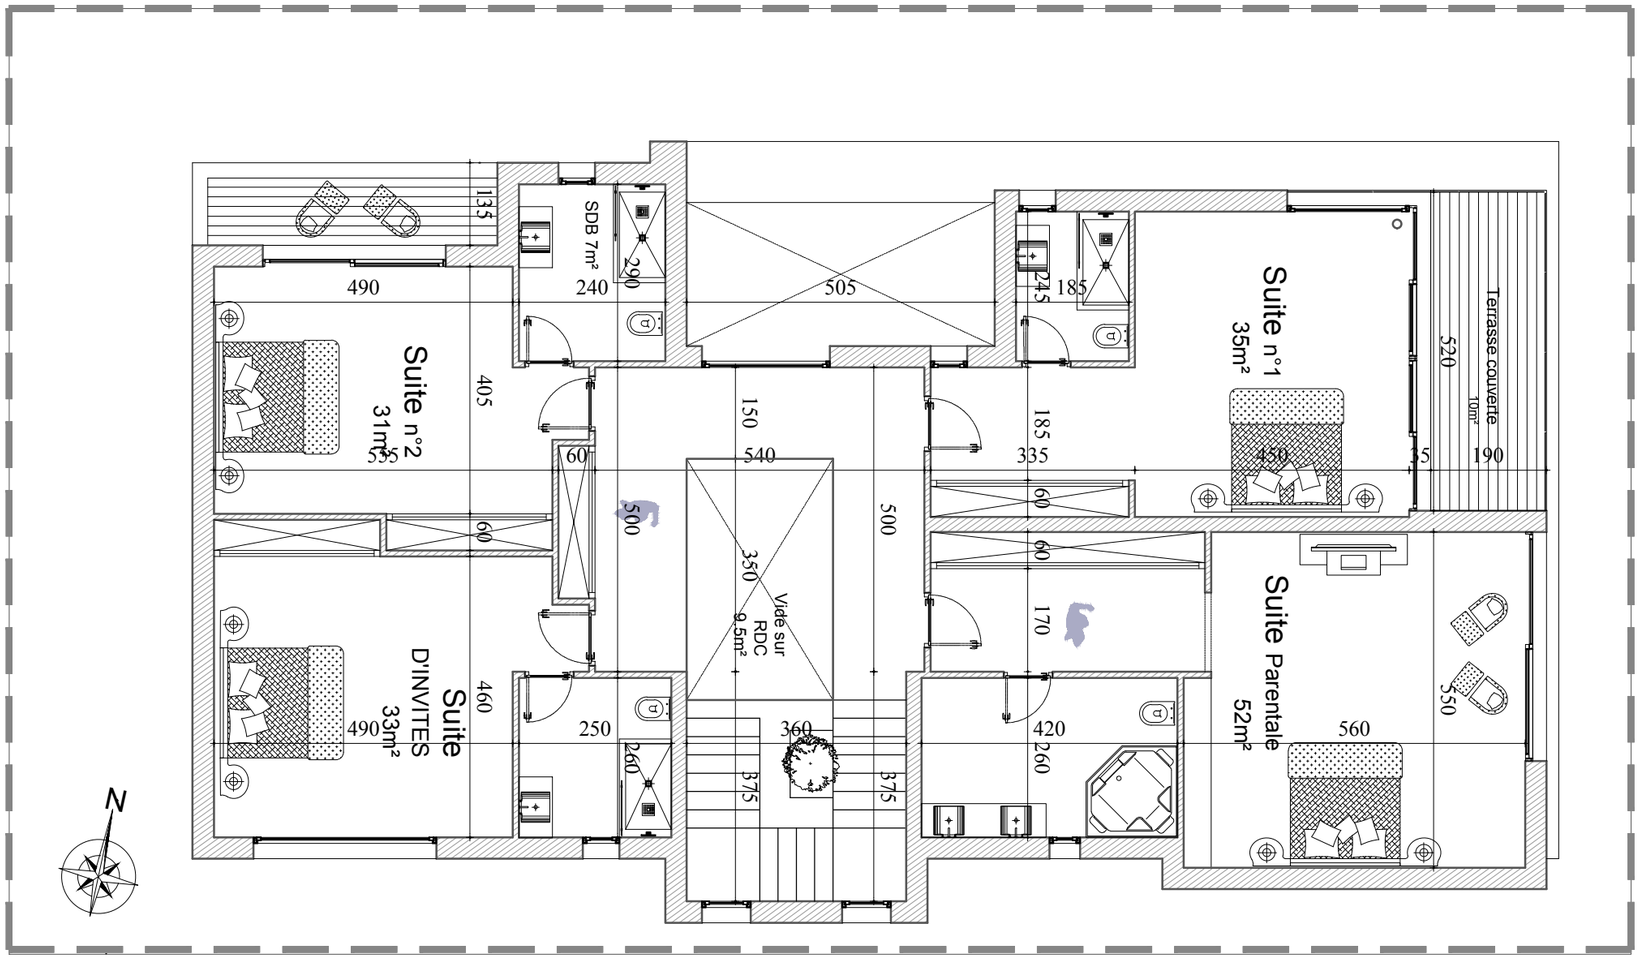

Plan Étage

Echelle 1/200

Villa 3	
Surface terrain	700 m²
Surface RDC	268,1 m²
Surface Etage	253,6 m²
Surface totale Couverte	521,7 m²

FAMILY COMPOUND

Chott Meriem - SOUSSE

Architectes: Marwen MTIMET
Anis BOUDEN

Villa 3

FAMILY COMPOUND

Chott Meriem - SOUSSE

Architectes: Marwen MTIMET
Anis BOUDEN

Villa 3

FAMILY COMPOUND

Chott Meriem - SOUSSE

Architectes: Marwen MTIMET
Anis BOUDEN

Villa 3

FAMILY COMPOUND

Chott Meriem - SOUSSE

Architectes: Marwen MTIMET
Anis BOUDEN

V

illa

FAMILY COMPOUND

Chott Meriem - SOUSSE

Architectes: Marwen MTIMET
Anis BOUDEN

Villa 4

N

Piscine

Jacuzzi

Séjour
21m²

410

510

45

440

500

Patio ouvert
24m²

35

Hall d'entrée
4.5m²

295

225

100

10

200

285

WC
8m²

200

35

610

SALON
46.5m²

Cheminée

1360

195

380

135

270

520

Cuisine
22.5m²

430

450

190

S.A.M
36.5m²

645

630

1060

Terrasse
34m²

Plan Rez De Chaussée

Echelle 1/50

FAMILY COMPOUND

Chott Meriem - SOUSSE

Architectes: Marwen MTIMET
Anis BOUDEN

Villa 4

Situation Repérage

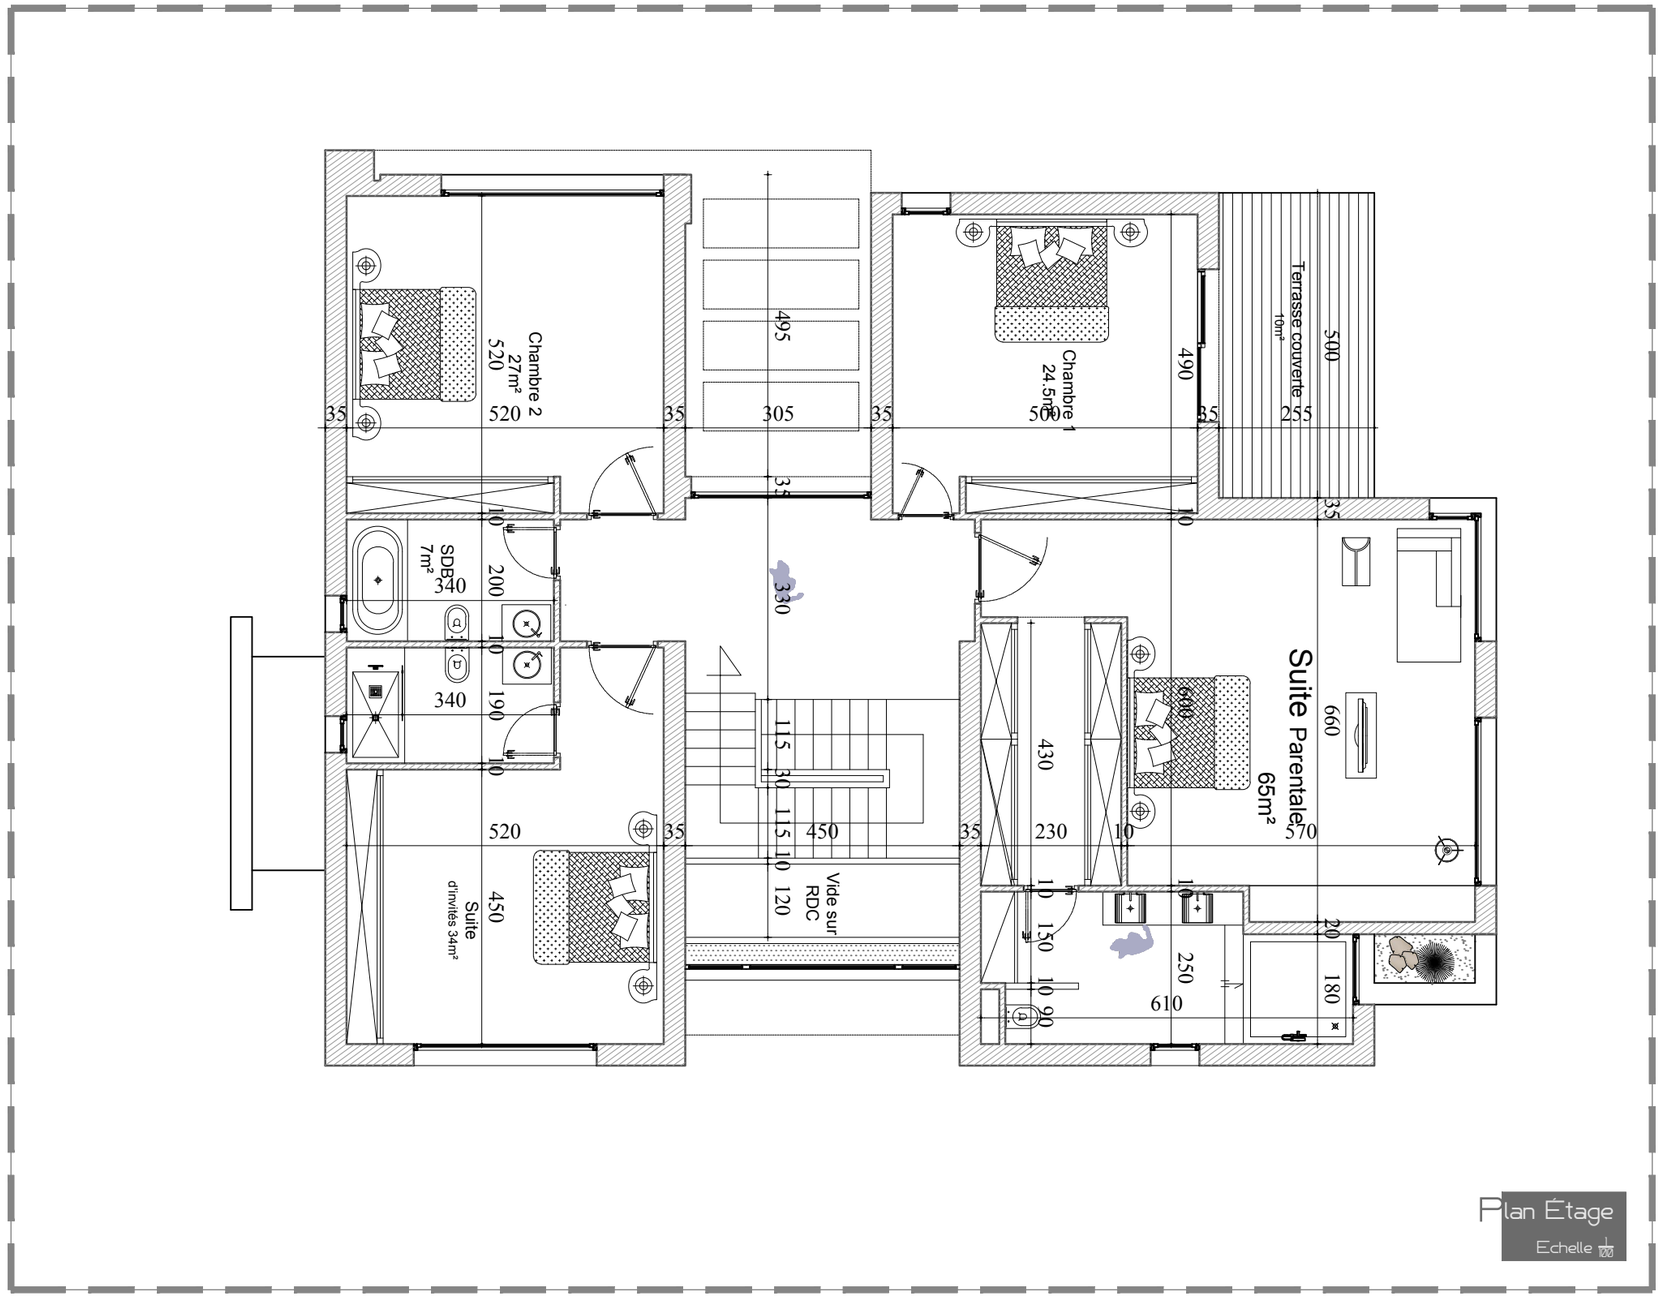

Villa 4	
Surface terrain	759,6 m²
Surface RDC	247,3 m²
Surface Etage	266,5 m²
Surface totale Couverte	513,8 m²

FAMILY COMPOUND

Chott Meriem - SOUSSE

Architectes: Marwen MTIMET
Anis BOUDEN

Villa 4

FAMILY COMPOUND

Chott Meriem - SOUSSE

Architectes: Marwen MTIMET
Anis BOUDEN

Villa 4

FAMILY COMPOUND

Chott Meriem - SOUSSE

Architectes: Marwen MTIMET
Anis BOUDEN

Villa 4

FAMILY COMPOUND

Chott Meriem - SOUSSE

Architectes: Marwen MTIMET
Anis BOUDEN

Villa

FAMILY COMPOUND

Chott Meriem - SOUSSE

Architectes: Marwen MTIMET
Anis BOUDEN

Villa 5

N

Jacuzzi

Piscine

WC 8.5m²

CHEMINEE

SALON 35m²

Cuisine 27.5m²

Hall d'entrée 15m²

Séjour 19m²

S.A.M 26m²

Plan Rez De Chaussée

FAMILY COMPOUND

Chott Meriem - SOUSSE

Architectes: Marwen MTIMET
Anis BOUDEN

Villa 5

Situation Repérage

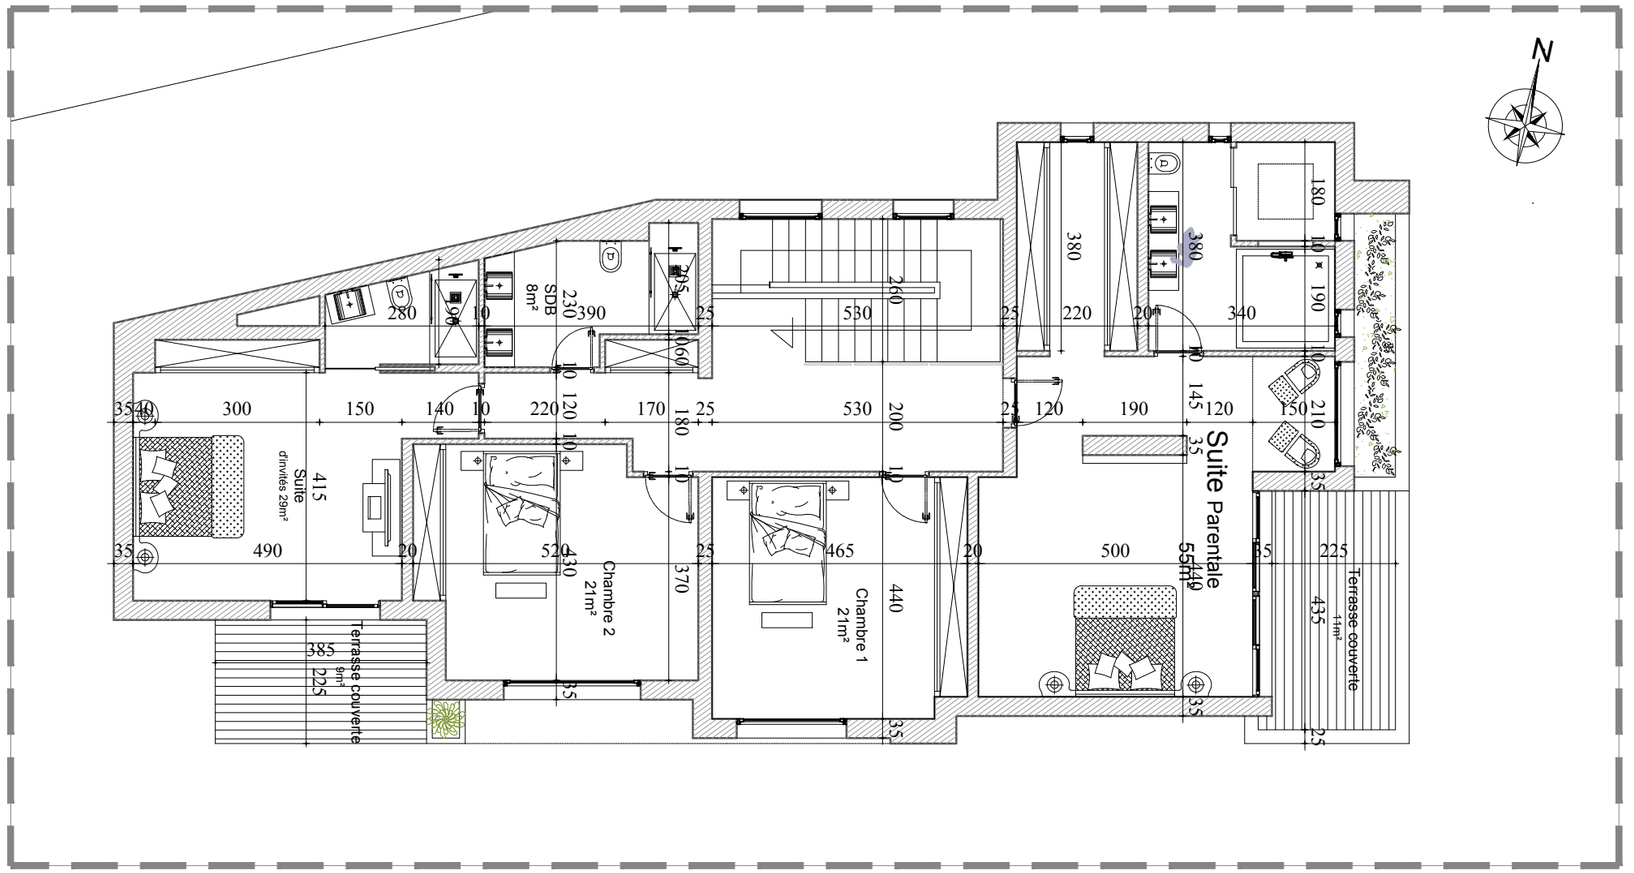

Plan Étage

Villa 5	
Surface terrain	703,4 m²
Surface RDC	221 m²
Surface Etage	225,2 m²
Surface totale Couverte	446,2 m²

FAMILY COMPOUND

Chott Meriem - SOUSSE

Architectes: Marwen MTIMET
Anis BOUDEN

Villa 5

FAMILY COMPOUND

Chott Meriem - SOUSSE

Architectes: Marwen MTIMET
Anis BOUDEN

Villa 5

FAMILY COMPOUND

Chott Meriem - SOUSSE

Architectes: Marwen MTIMET
Anis BOUDEN

Villa 5

FAMILY COMPOUND

Chott Meriem - SOUSSE

Architectes: Marwen MTIMET
Anis BOUDEN