RÉPUBLIQUE ALGÉRIENNE DÉMOCRATIQUE ET POPULAIRE

CONCEPTION D'UN HÔTEL SPA

Commune de YAKOUREN, Wilaya de TIZI OUZOU, L'ALGERIE

MANDATAIRE: Monsieur Jamal ARIB

MARS 2017

Architectes: Anis BOUDEN
Ilyes DARGHOUTH

B.D Architectes

Adresse: 24 Avenue d'Afrique, Menzah 5, Ariana, TUNISIE
Tél/Fax: (+216) 71 232 956 GSM: (+216) 50 245 344
Mail: boudenanis@gmail.com

Phase d'étude: APS Avant Projet Sommaire

RAPPORT DE L'ARCHITECTE

YAKOUREN, TIZI OUZOU, L'ALGERIE

YAKOUREN, est une commune de la wilaya de TIZI OUZOU, en KABYLIE, située à 46 km à l'est de Tizi Ouzou et à 11 km à l'est d'Azazga. La commune fait partie du Âarch Aït Ghobri.

Les forêts de Yakouren sont propices aux randonnées sportives, les séjours écologiques et culturels. La faune endémique de la région est assez riche, celle de giboyeuse en particulier (Sangliers, lièvres, Perdrix, étourneaux, grives et divers oiseaux de proie). L'attraction principal reste sans doute le singe magot, très prolifique dans les forêts de Yakouren.
Le beau massif forestier est riche en chênes, lièges et races de singes attirant les visiteurs.
Les visiteurs peuvent également apprécier l'exposition d'objets artisanaux se trouvant tout au long de la route nationale ainsi que les fontaines fraîches s'offrant à eux tout au long de leur randonnée.

Le charme de YAKOUREN fait d'elle un lieu privilégié pour de nombreux vacanciers avide de calme et de beaux paysages.

B.D Architectes
Architectes: Anis BOUDEN
Ilyes DARGHOUTH
Adresse: 24 Avenue d'Afrique, Menzah 5, Ariana
Tél/Fax: (+216) 71 232 956 GSM: (+216) 50 245 344
Mail: boudenanis@gmail.com

CONCEPTION D'UN HÔTEL SPA
YAKOUREN - TIZI OUZOU - ALGÉRIE
Mandataire: Monsieur Jamal ARIB

Cadre Geographique

MARS 2017

CADRE DU PROJET

Les atouts géographique, naturel, forestier et climatique sont propices au développement d'un tourisme adéquat à la zone.

A cet effet, Le promoteur se propose de créer un Hotel SPA ayant des activités ludiques, aquatiques, de détente et de repos.

TERRAIN & VOISINAGE

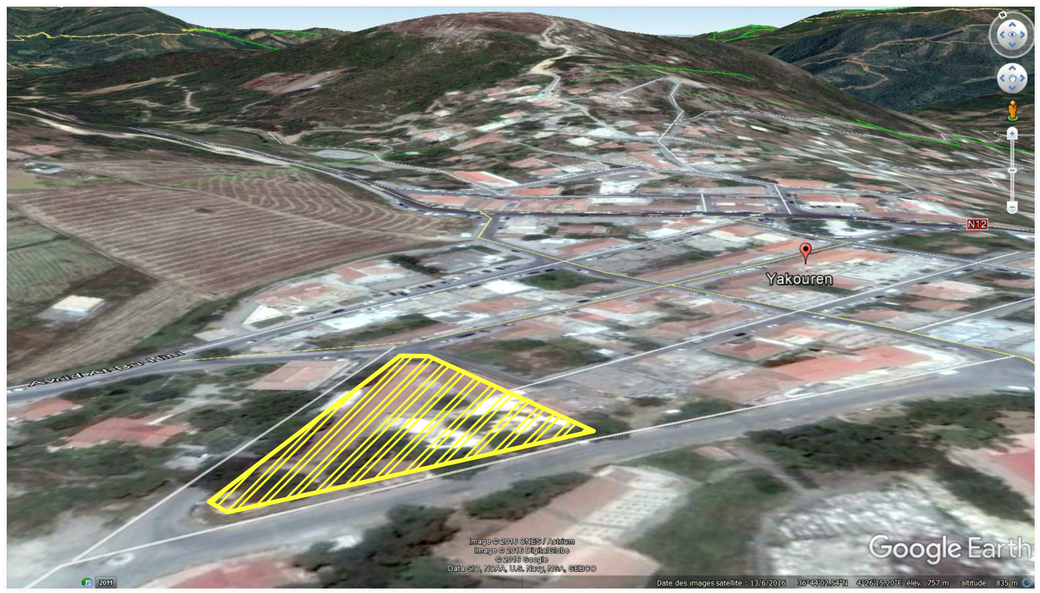

CONTEXTE URBAIN ET NATUREL

A l'image de la plupart des villages de Kabilye, l'environnement urbain de Yakouren est rural montagnard; constitué de bâtiments qui adoptent les configurations des crêtes naturelles.

Les matériaux de construction dominants dans le paysage architectural sont: les tuiles pignons triangulaires, les pierres naturelles et le bois (liège).

ASSIETTE DU PROJET

D'une surface de 2750 m², le terrain est situé à l'ouest de Yakouren.

Le terrain est de forme triangulaire et donnant sur 3 rues; les rues du cotés nord desservent le centre ville.

COMPOSANTES DU PROJET

1	**Espaces Commun**	
a	Réception et Salons d'accueil	
b	Salle Polyvalente	
c	Restaurant	
d	Tisanerie et Salons de détente	
2	**Zone SPA & BIEN ETRE**	
a	Accueil & Vestiaires	
b	Dry Massage	
c	Esthétique & coiffure	
d	Salle de Sport	
e	Piscines	
f	Hammam	
g	Sauna & hydro massages	
3	**Hébergement**	
a	36 Chambres Type 1	
b	40 Chambres Type 2	
c	8 Suites	
d	Solarium	
4	**Administration**	
a	Bureau de direction	
b	Bureau chef Personnel	
c	Bureau Financiers	
d	Comptabilit é & Marketing	
e	Bureau Chef r é ception & Bagagerie	
5	**Locaux de Services**	
a	Buanderie & Linge propre	
b	Infirmerie	
c	Bureau Chef Maintenance	
d	Cuisine Personnel & R é fectoire	
e	Locaux Techniques & Chaufferie	
6	**Stationnement**	
a	51 Places de Parking	

B.D Architectes
Architectes: Anis BOUDEN
Ilyes DARGHOUTH
Adresse: 24 Avenue d'Afrique, Menzah 5, Ariana
Tél/Fax: (+216) 71 232 956 GSM: (+216) 50 245 344
Mail: boudenanis@gmail.com

CONCEPTION D'UN HÔTEL SPA
YAKOUREN - TIZI OUZOU - ALGÉRIE
Mandataire: Monsieur Jamal ARIB

Terrain & Cadre du Projet

MARS 2017

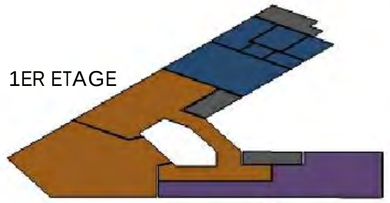

Par souci de fonctionnalité les espaces de services et administration sont superposés dans tous les étages afin de permettre une meilleure fluidité de circulation pour le personnel de l'hotel sans nuire aux usagers et aux résidents.

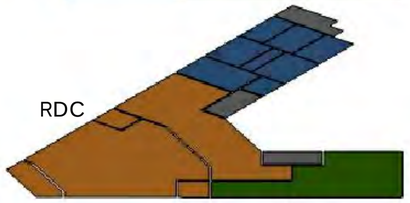

L'accès des véhicules et le stationnement se font au 2ème sous sol via le rond point existant qui se trouve au niveau le plus bas du terrain, permettant ainsi de créer un 1er sous sol qui abritera les piscines et le hammam sans pour autant dépasser en hauteur le point le plus haut du terrain.

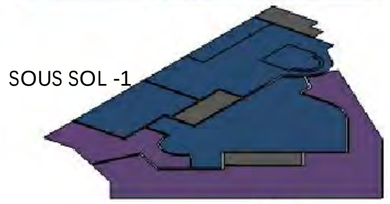

Ce 2ème sous sol permet le stationnement de 51 véhicules ainsi qu'une plateforme de ravitaillement de service pour tout l'hotel.

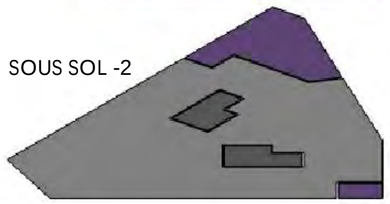

Le 1er sous sol reste quand meme aéré sur le coté Nord par des fenetres hautes et sur le coté sud via une ruelle creusée dans le terrain qui fait office d'une grande cours anglaise.

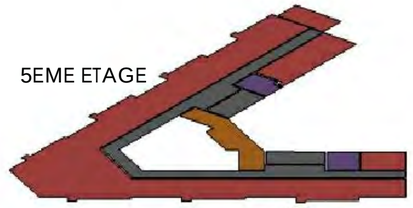

Les 4 étages d'hébergement comportent 76 chambres et 8 suites (2 suites à chaque étage).

Les chambres sont de 2 types, le type 1 de 32m² de superficie contiennent une cabine privative de massage , le type 2 est de 30m² .

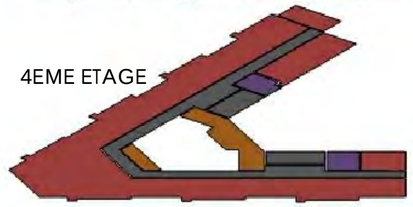

Chacun des 4 étages d'hébergement contient des offices des locaux annexes pour améliorer la qualité de service aux usagers.

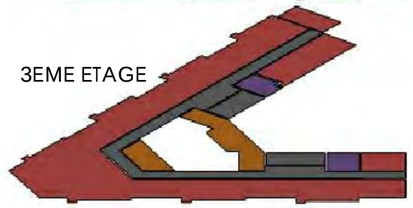

A l'aboutissement de l'aile Nord, se trouve à chaque étage un solarium accessible aux usagers pour se relaxer , cet espace possède une vue dégagée sur les reliefs de la zone , ce qui lui donne un caractère relaxant.

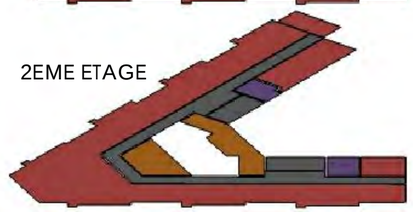

Ces étages sont desservis par 2 batteries d'escaliers et de double ascenseurs, depuis le 2ème sous sol jusqu'au dernier étage de l'hotel, et débouchant chacun sur un dégagement.

1	**Espaces Commun**
a	Réception et Salons d'accueil
b	Salle Polyvalente
c	Restaurant
d	Tisanerie et Salons de détente
2	**Zone SPA & BIEN ETRE**
a	Accueil & Vestiaires
b	Dry Massage
c	Esthétique & coiffure
d	Salle de Sport
e	Piscines
f	Hammam
g	Sauna & hydro massages
3	**Hébergement**
a	Chambres Type 1
b	Chambres Type 2
c	Suite
d	Solarium
4	**Administration**
a	Bureau de direction
b	Bureau chef Personnel
c	Bureau Financiers
d	Comptabilité & Marketing
e	Bureau Chef réception & Bagagerie
5	**Locaux de Services**
a	Buanderie & Linge propre
b	Infirmerie
c	Bureau Chef Maintenance
d	Cuisine Personnel & Réfectoire
e	Locaux Techniques & Chaufferie
6	**Stationnement**
a	51 Places de Parking

Espaces Communs

Zone SPA et Bien Etre

Hébergement

Administration

Locaux de service

Stationnement

Circulations

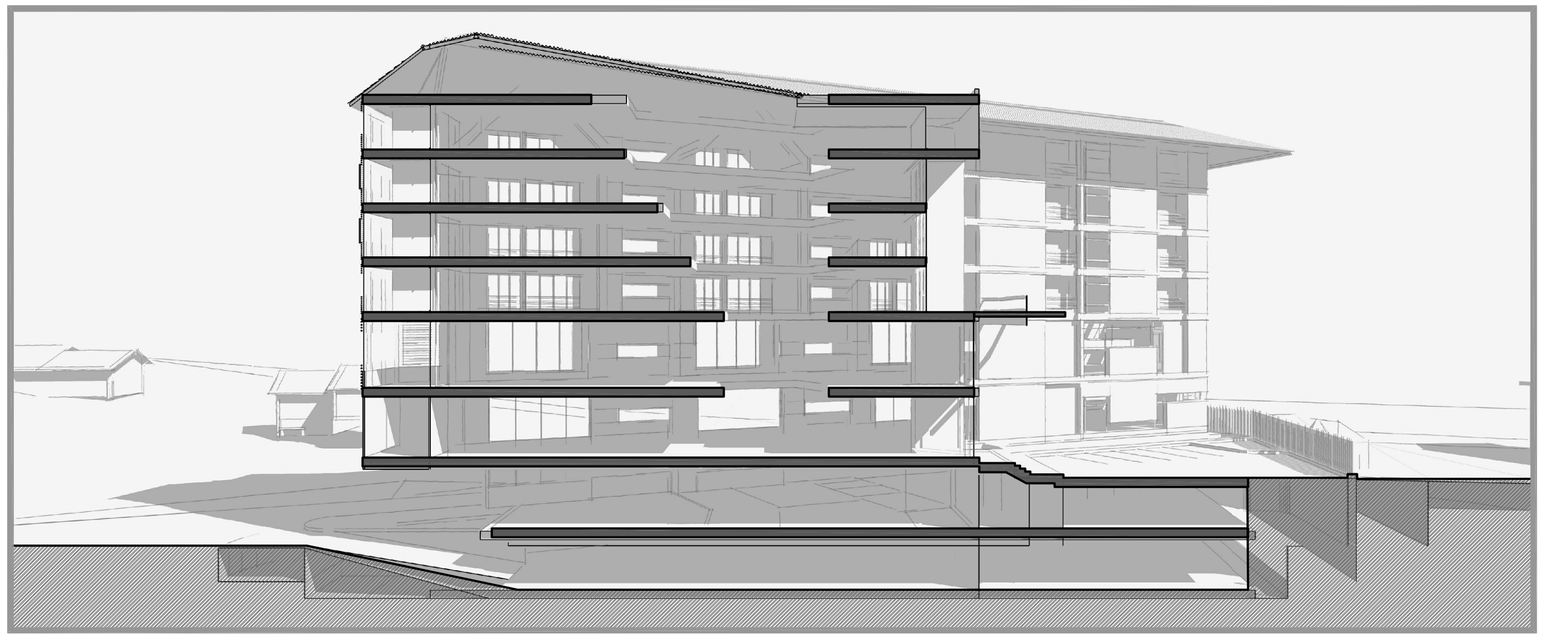

Un vide sur rez de chaussée existe dans tous les étages d'hébergement, autour du quel s'articulent des espaces de circulation , de rencontre et de détente, permettant ainsi une grande convivialité.

A chaque fois qu'on monte d'un étage le vide sur rez de chaussée s'élargit, permettant ainsi un meilleur éclairage naturel et une impression de grandeur , ce vide sera ponctué à chaque étage d'un jardin suspendu rappelant la nature meme à l'intérieur du projet.

B.D Architectes
Architectes: Anis BOUDEN
Ilyes DARGHOUTH
Adresse: 24 Avenue d'Afrique, Menzah 5, Ariana
Tél/Fax: (+216) 71 232 956 GSM: (+216) 50 245 344
Mail: boudenanis@gmail.com

CONCEPTION D'UN HÔTEL SPA

YAKOUREN - TIZI OUZOU - ALGÉRIE

Mandataire: Monsieur Jamal ARIB

Epannelage Fonctionnel

MARS 2017

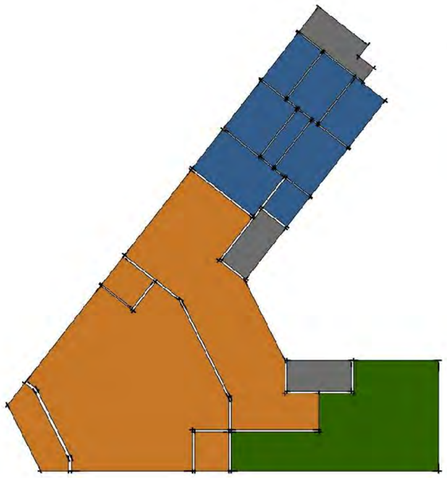

- Espaces Communs
- Zone SPA et Bien Etre
- Hébergement
- Administration
- Locaux de service
- Stationnement
- Circulations

-4.08

0.00

Entrée

0.20

proprieté privée

Entrée secondaire

-4.08

-3.90

vers vervour

+1.53 vers centre ville

Massage

Massage

Massage

Massage

Vestiaire H

Vestiaire F

Vestiaire Pers

Acceuil SPA

Office

Bar à Jus

Accueil

Salle polyvalente

Scène

Local Technique

Loge Artistes

réception

Local Service

Bureau Chef réception

Bagagerie

Caisse

Bureau Financiers

Bureau de direction

Bureau Chef Personnel & Pointage

Open Space Comptabilité & Marketing

Monte Charge

Table de 10

B.D Architectes

Architectes: Anis BOUDEN
Ilyes DARGHOUTH

Adresse: 24 Avenue d'Afrique, Menzah 5, Ariana
Tél/Fax: (+216) 71 232 956 GSM: (+216) 50 245 344
Mail: boudenanis@gmail.com

CONCEPTION D'UN HÔTEL SPA

YAKOUREN - TIZI OUZOU - ALGÉRIE

Mandataire: Monsieur Jamal ARIB

Plan RDC 1/200

MARS 2017

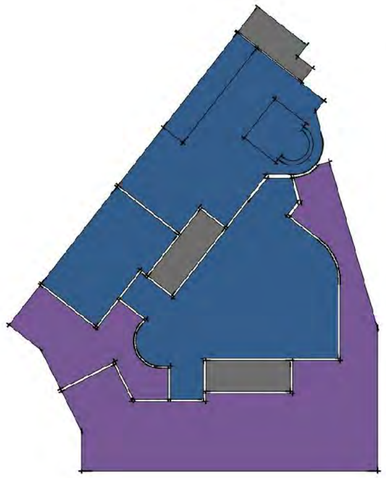

- Espaces Communs
- Zone SPA et Bien Etre
- Hébergement
- Administration
- Locaux de service
- Stationnement
- Circulations

B.D Architectes

Architectes: Anis BOUDEN
Ilyes DARGHOUTH

Adresse: 24 Avenue d'Afrique, Menzah 5, Ariana
Tél/Fax: (+216) 71 232 956 GSM: (+216) 50 245 344
Mail: boudenanis@gmail.com

CONCEPTION D'UN HÔTEL SPA

YAKOUREN - TIZI OUZOU - ALGÉRIE

Mandataire: Monsieur Jamal ARIB

Plan Sous Sol -1 — 1/200

MARS 2017

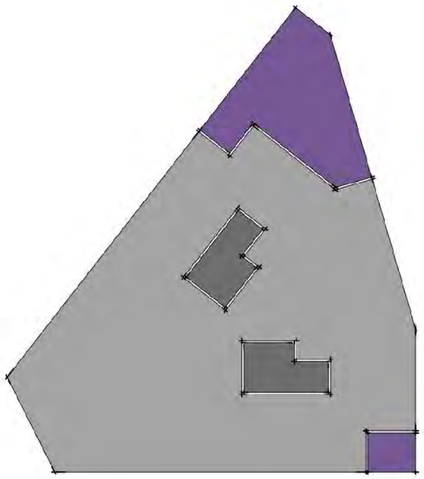

- Espaces Communs
- Zone SPA et Bien Etre
- Hébergement
- Administration
- Locaux de service
- Stationnement
- Circulations

B.D Architectes

Architectes: Anis BOUDEN
Ilyes DARGHOUTH

Adresse: 24 Avenue d'Afrique, Menzah 5, Ariana
Tél/Fax: (+216) 71 232 956 GSM: (+216) 50 245 344
Mail: boudenanis@gmail.com

CONCEPTION D'UN HÔTEL SPA

YAKOUREN - TIZI OUZOU - ALGÉRIE

Mandataire: Monsieur Jamal ARIB

Plan Sous Sol -2

1/200

MARS 2017

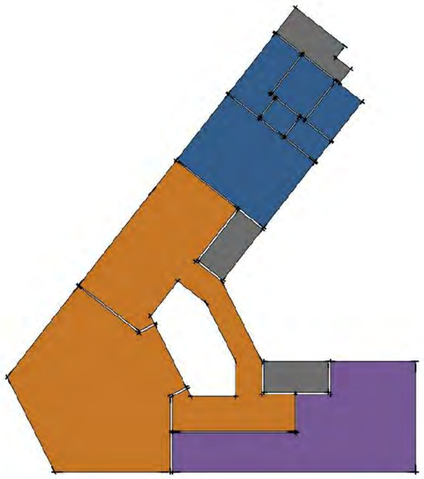

- Espaces Communs
- Zone SPA et Bien Etre
- Hébergement
- Administration
- Locaux de service
- Stationnement
- Circulations

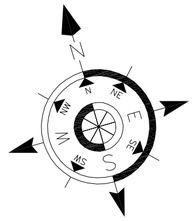

B.D Architectes

Architectes: Anis BOUDEN
Ilyes DARGHOUTH

Adresse: 24 Avenue d'Afrique, Menzah 5, Ariana
Tél/Fax: (+216) 71 232 956 GSM: (+216) 50 245 344
Mail: boudenanis@gmail.com

CONCEPTION D'UN HÔTEL SPA

YAKOUREN - TIZI OUZOU - ALGÉRIE

Mandataire: Monsieur Jamal ARIB

Plan 1er Etage 1/200

MARS 2017

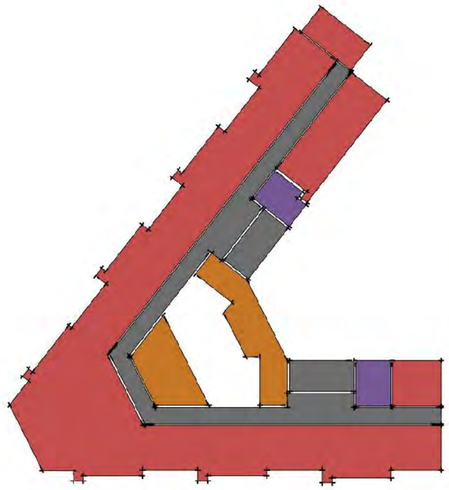

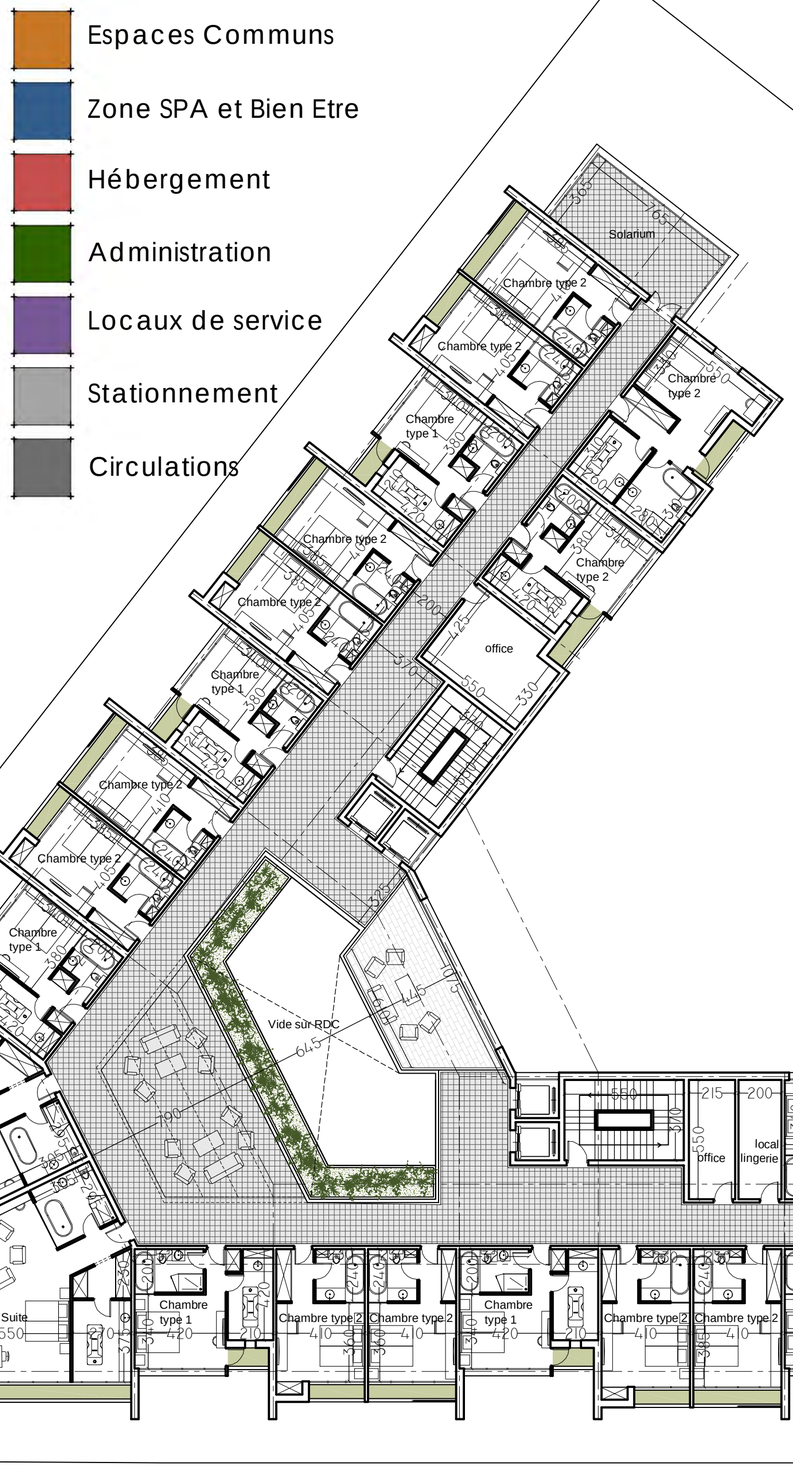

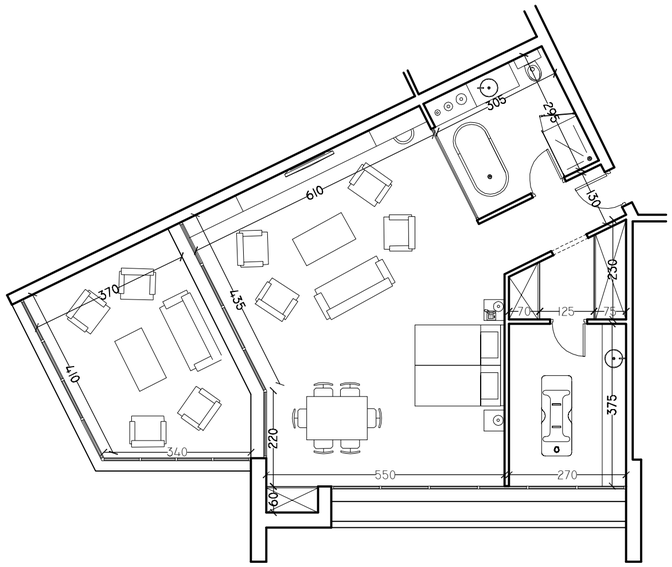

Suite Type
échelle 1/100

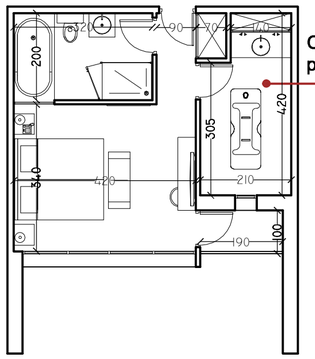

Chambre Type 1
échelle 1/100

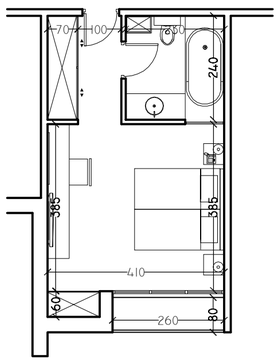

Chambre Type 2
échelle 1/100

Architectes: Anis BOUDEN
Ilyes DARGHOUTH
Adresse: 24 Avenue d'Afrique, Menzah 5, Ariana
Tél/Fax: (+216) 71 232 956 GSM: (+216) 50 245 344
Mail: boudenanis@gmail.com

CONCEPTION D'UN HÔTEL SPA

YAKOUREN - TIZI OUZOU - ALGÉRIE

Mandataire: Monsieur Jamal ARIB

Plan Etage courant (étages 2, 3, 4 et 5)

1/200

MARS 2017

IMAGE DU PROJET

Le projet a été conçu de manière a s'intégrer dans le cadre urbain et surtout naturel qui caractérise la zone, à savoir le cadre rural montagnard.
Les matériaux de construction dominants sont: les tuiles pignons triangulaires, les pierres naturelles et le bois (liège).

B.D Architectes
Architectes: Anis BOUDEN
Ilyes DARGHOUTH
Adresse: 24 Avenue d'Afrique, Menzah 5, Ariana
Tél/Fax: (+216) 71 232 956 GSM: (+216) 50 245 344
Mail: boudenanis@gmail.com

CONCEPTION D'UN HÔTEL SPA
YAKOUREN - TIZI OUZOU - ALGÉRIE
Mandataire: Monsieur Jamal ARIB

VUE GÉNÉRALE

MARS 2017

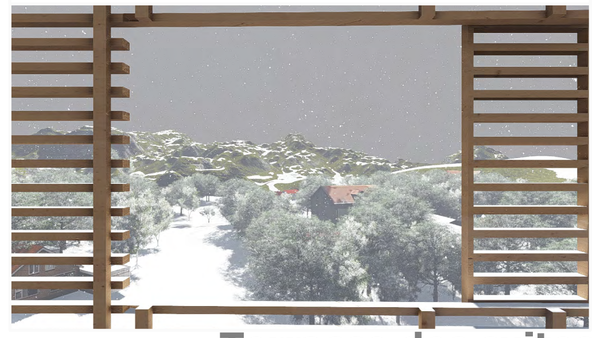

Terrasse des suites

B.D Architectes
Architectes: Anis BOUDEN
Ilyes DARGHOUTH
Adresse: 24 Avenue d'Afrique, Menzah 5, Ariana
Tél/Fax: (+216) 71 232 956 GSM: (+216) 50 245 344
Mail: boudenanis@gmail.com

CONCEPTION D'UN HÔTEL SPA

YAKOUREN - TIZI OUZOU - ALGÉRIE

Mandataire: Monsieur Jamal ARIB

VUES SÉQUENTIELLES

MARS 2017

Façades

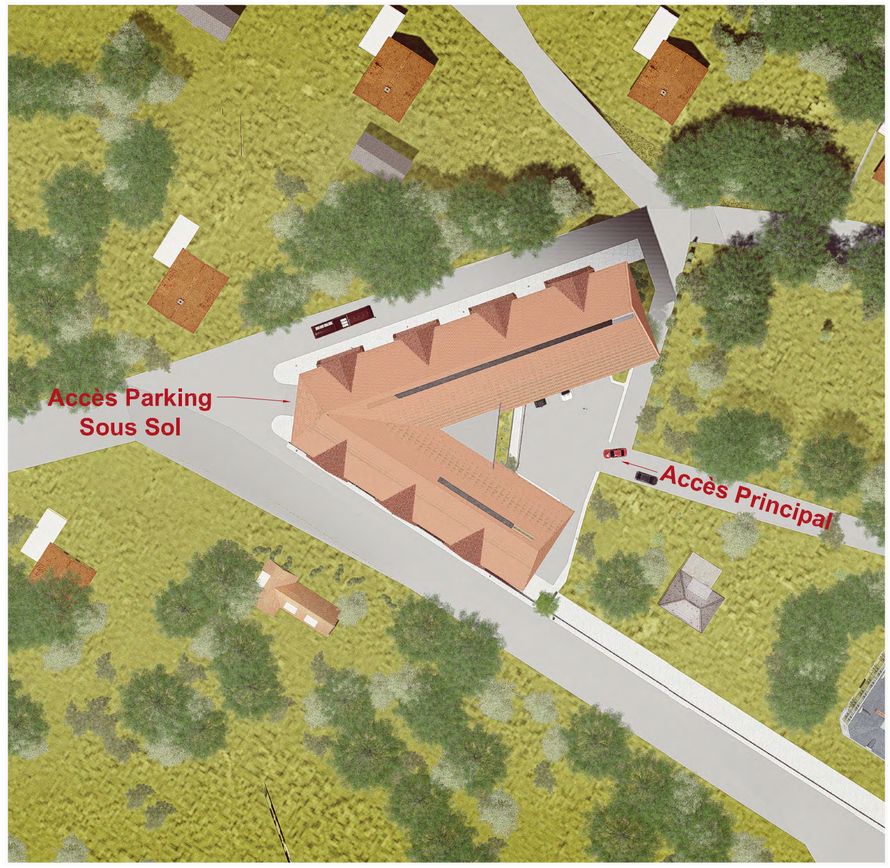

Plan des Masses

B.D Architectes
Architectes: Anis BOUDEN
Ilyes DARGHOUTH
Adresse: 24 Avenue d'Afrique, Menzah 5, Ariana
Tél/Fax: (+216) 71 232 956 GSM: (+216) 50 245 344
Mail: boudenanis@gmail.com

CONCEPTION D'UN HÔTEL SPA

YAKOUREN - TIZI OUZOU - ALGÉRIE

Mandataire: Monsieur Jamal ARIB

VUES SÉQUENTIELLES

MARS 2017

Façades

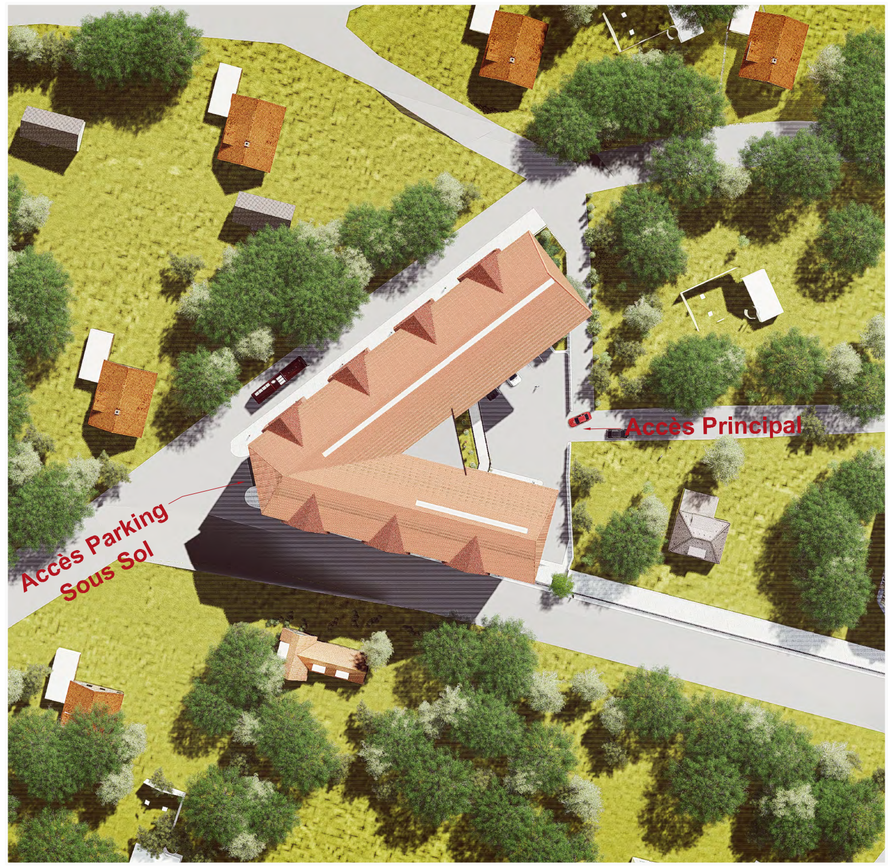

Plan des Masses

B.D Architectes
Architectes: Anis BOUDEN
Ilyes DARGHOUTH
Adresse: 24 Avenue d'Afrique, Menzah 5, Ariana
Tél/Fax: (+216) 71 232 956 GSM: (+216) 50 245 344
Mail: boudenanis@gmail.com

CONCEPTION D'UN HÔTEL SPA

YAKOUREN - TIZI OUZOU - ALGÉRIE

Mandataire: Monsieur Jamal ARIB

VUES SÉQUENTIELLES

MARS 2017

B.D Architectes

Architectes: Anis BOUDEN
Ilyes DARGHOUTH

Adresse: 24 Avenue d'Afrique, Menzah 5, Ariana
Tél/Fax: (+216) 71 232 956 GSM: (+216) 50 245 344
Mail: boudenanis@gmail.com

CONCEPTION D'UN HÔTEL SPA

YAKOUREN - TIZI OUZOU - ALGÉRIE

Mandataire: Monsieur Jamal ARIB

VUES SÉQUENTIELLES

MARS 2017

AMBIANCE SOUHAITÉE

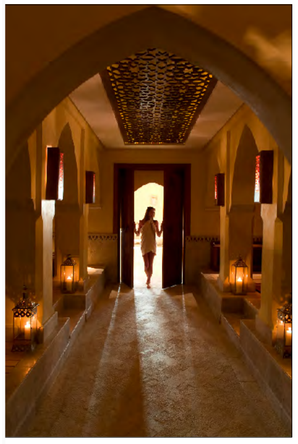

HAMMAM

SAUNA ET DÉTENTE

BASSIN PRIVATIF

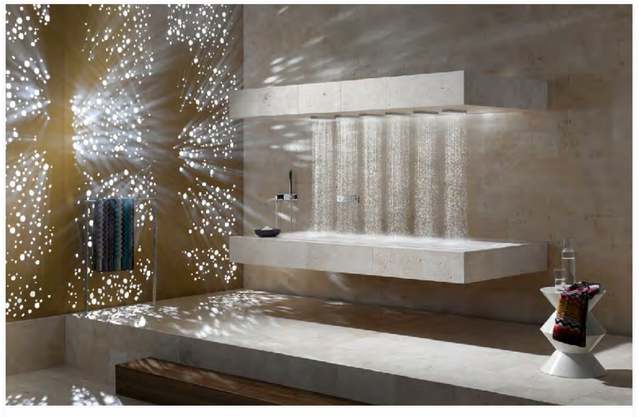

DOUCHE SOUS AFFUSION

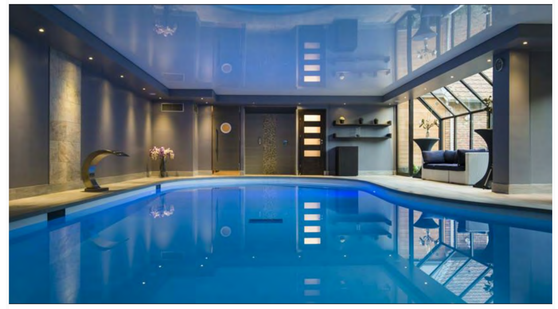

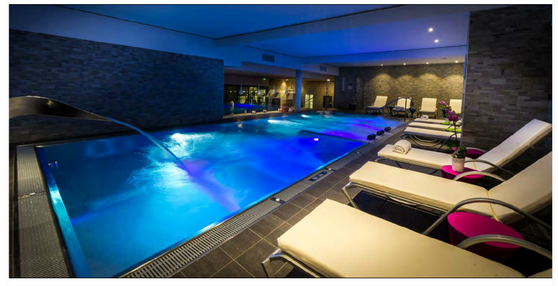

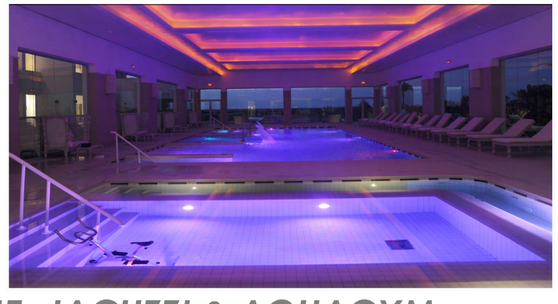

PISCINE, JACUZZI & AQUAGYM

B.D Architectes
Architectes: Anis BOUDEN
Ilyes DARGHOUTH
Adresse: 24 Avenue d'Afrique, Menzah 5, Ariana
Tél/Fax: (+216) 71 232 956 GSM: (+216) 50 245 344
Mail: boudenanis@gmail.com

CONCEPTION D'UN HÔTEL SPA

YAKOUREN - TIZI OUZOU - ALGÉRIE

Mandataire: Monsieur Jamal ARIB

Activités Proposées

MARS 2017

N	Désignation		S. Net Unitaire	S. Nett Total	S. Brut
I	**Sous Sol -2**				
1	51 Place de Parking	1	664	664	
2	Circulation Vehiculaire	1	386	386	
3	Baches à eau et locaux techniques	1	220	220	
	Circulation verticale	1	150	150	
	Circulation horizontale	1	202	202	
	TOTAL			1622	1794
II	**Sous Sol -1**				
1	Piscines et Plages	1	320	320	
2	Hammam	1	376	376	
3	Sauna & Hydro Massages	1	132	132	
4	Locaux Techniques	1	234	234	
5	Espace Personnels (vestiaires et bureaux)	1	354	354	
	TOTAL			1416	1642
III	**Rez De Chaussée**				
1	Reception & Salons d'acceuil	1	328	328	
2	Salle Polyvalente	1	463	463	
3	Zone Spa	1	311	311	
4	Administration	1	241	241	
	TOTAL			1343	1472
IV	**Etage 1**				
1	Tisannerie et Salons de détente	1	338	338	
2	Restaurant	1	322	322	
3	Zone Spa	1	291	291	
4	Locaux annexes (cuisines et depots)	1	261	261	
5	Vide sur RDC	1	76	76	
	TOTAL			1288	1472
V	**Etages Courant 2, 3, 4 et 5**				
1	Chambre Type 1	9	32	288	
2	Chambre Type 2	10	30	300	
3	Suites	2	106	212	
4	Circulation	1	345	345	
5	Locaux annexes	1	46	46	
6	Solarium	1	33	33	
	TOTAL PAR ETAGE			1224	1598
	TOTAL ETAGES COURANT (4 étages)			4896	6392
	Total Général Surface Couverte				**12772**

Surface Terrain: 2750 m²
Surface Couverte (Emprise au sol): 1472m²
Surface Couverte Totale: 12772m²

B.D Architectes
Architectes: Anis BOUDEN
Ilyes DARGHOUTH
Adresse: 24 Avenue d'Afrique, Menzah 5, Ariana
Tél/Fax: (+216) 71 232 956 GSM: (+216) 50 245 344
Mail: boudenanis@gmail.com

CONCEPTION D'UN HÔTEL SPA

YAKOUREN - TIZI OUZOU - ALGÉRIE

Mandataire: Monsieur Jamal ARIB

PROGRAMME & SURFACES

MARS 2017