


COUPE A-A ech 1/200



COUPE B-B ech 1/200

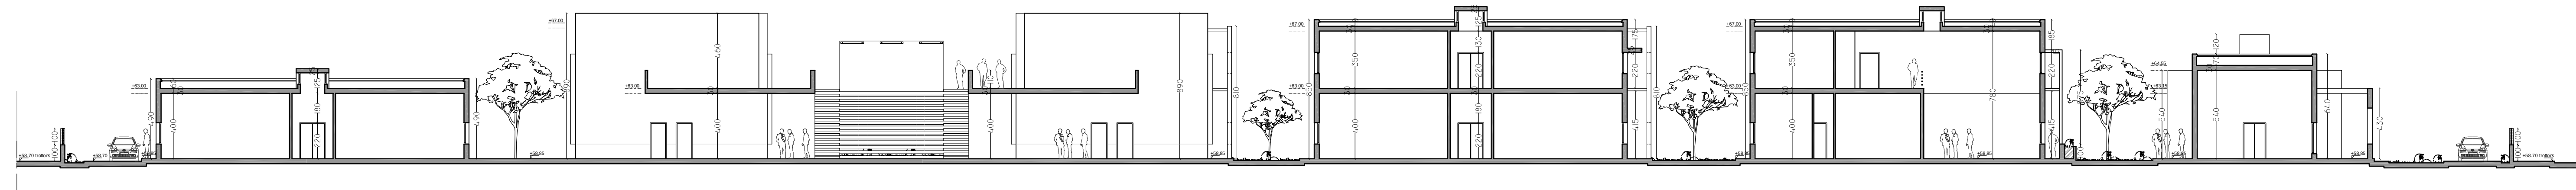

FACADE SUD EST ech 1/200



FACADE SUD OUEST ech 1/200

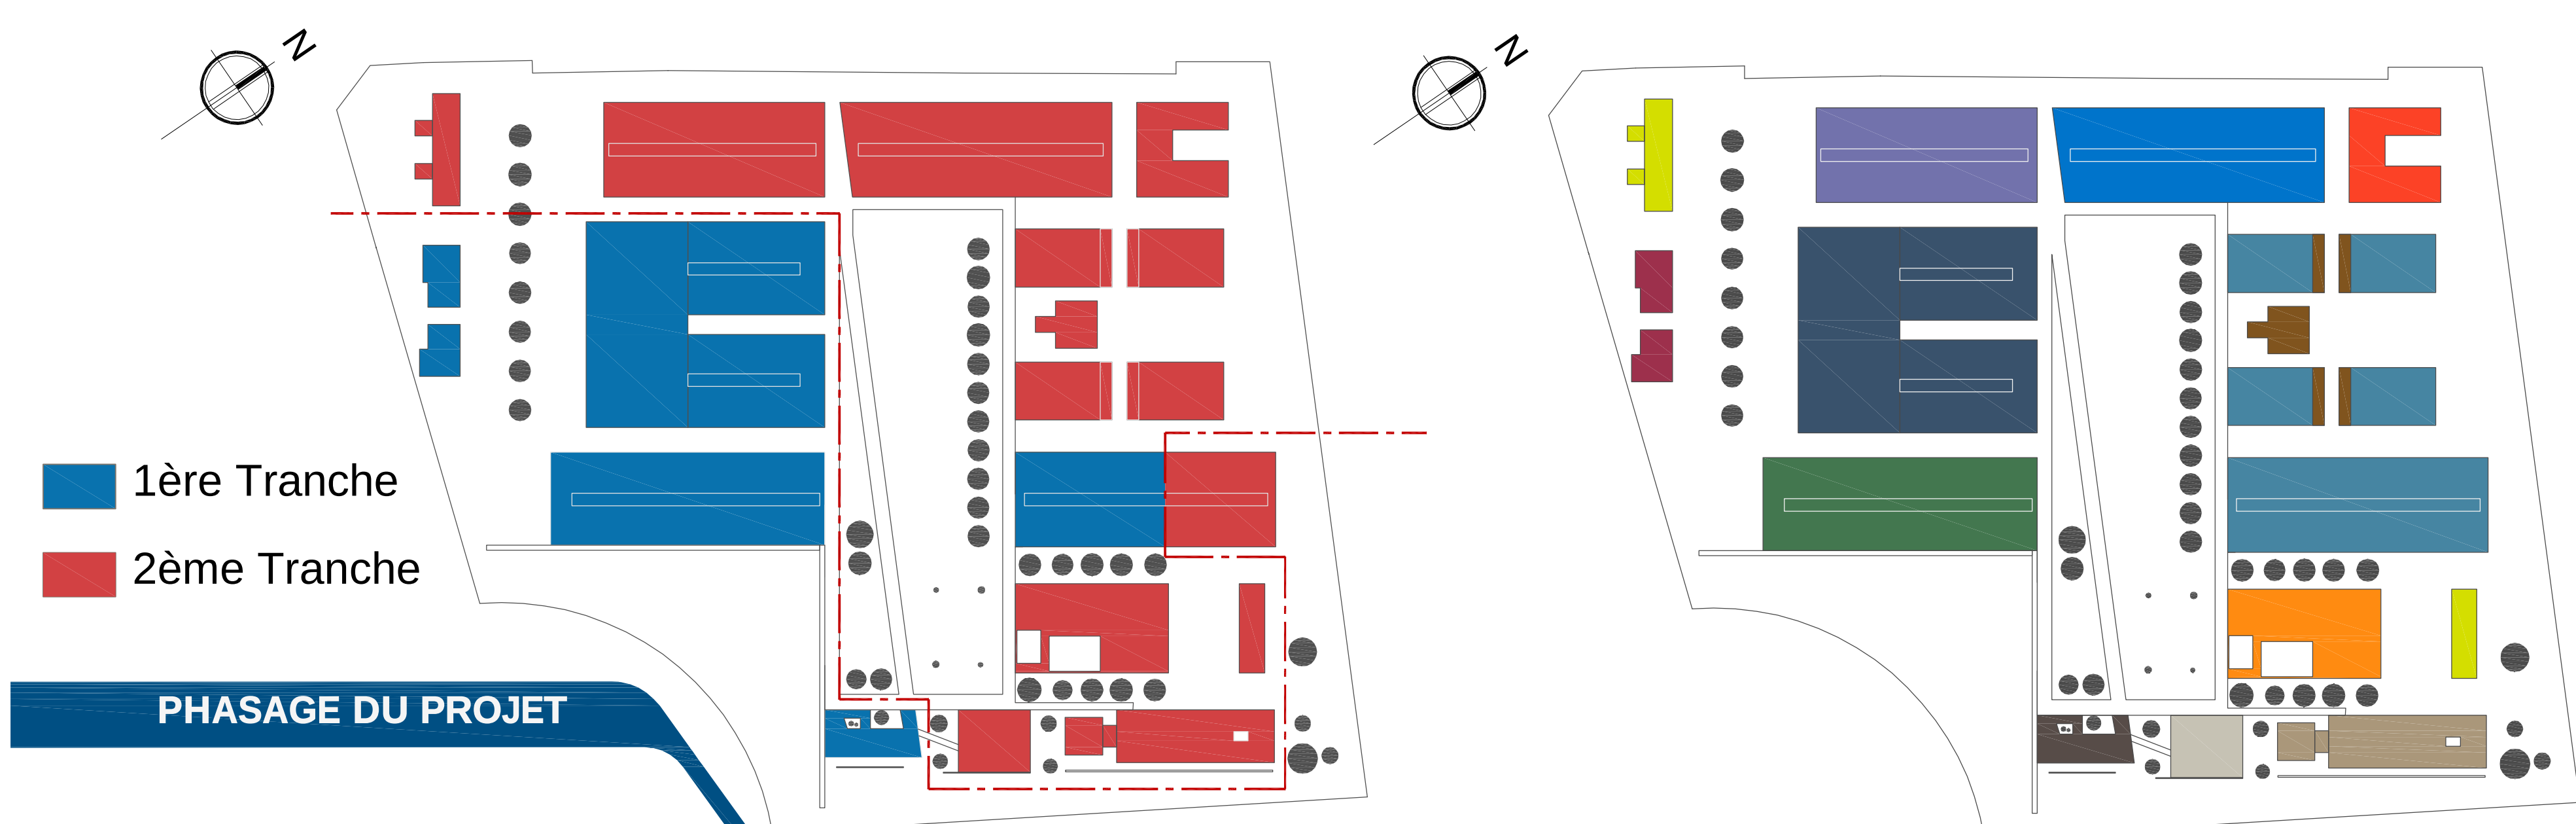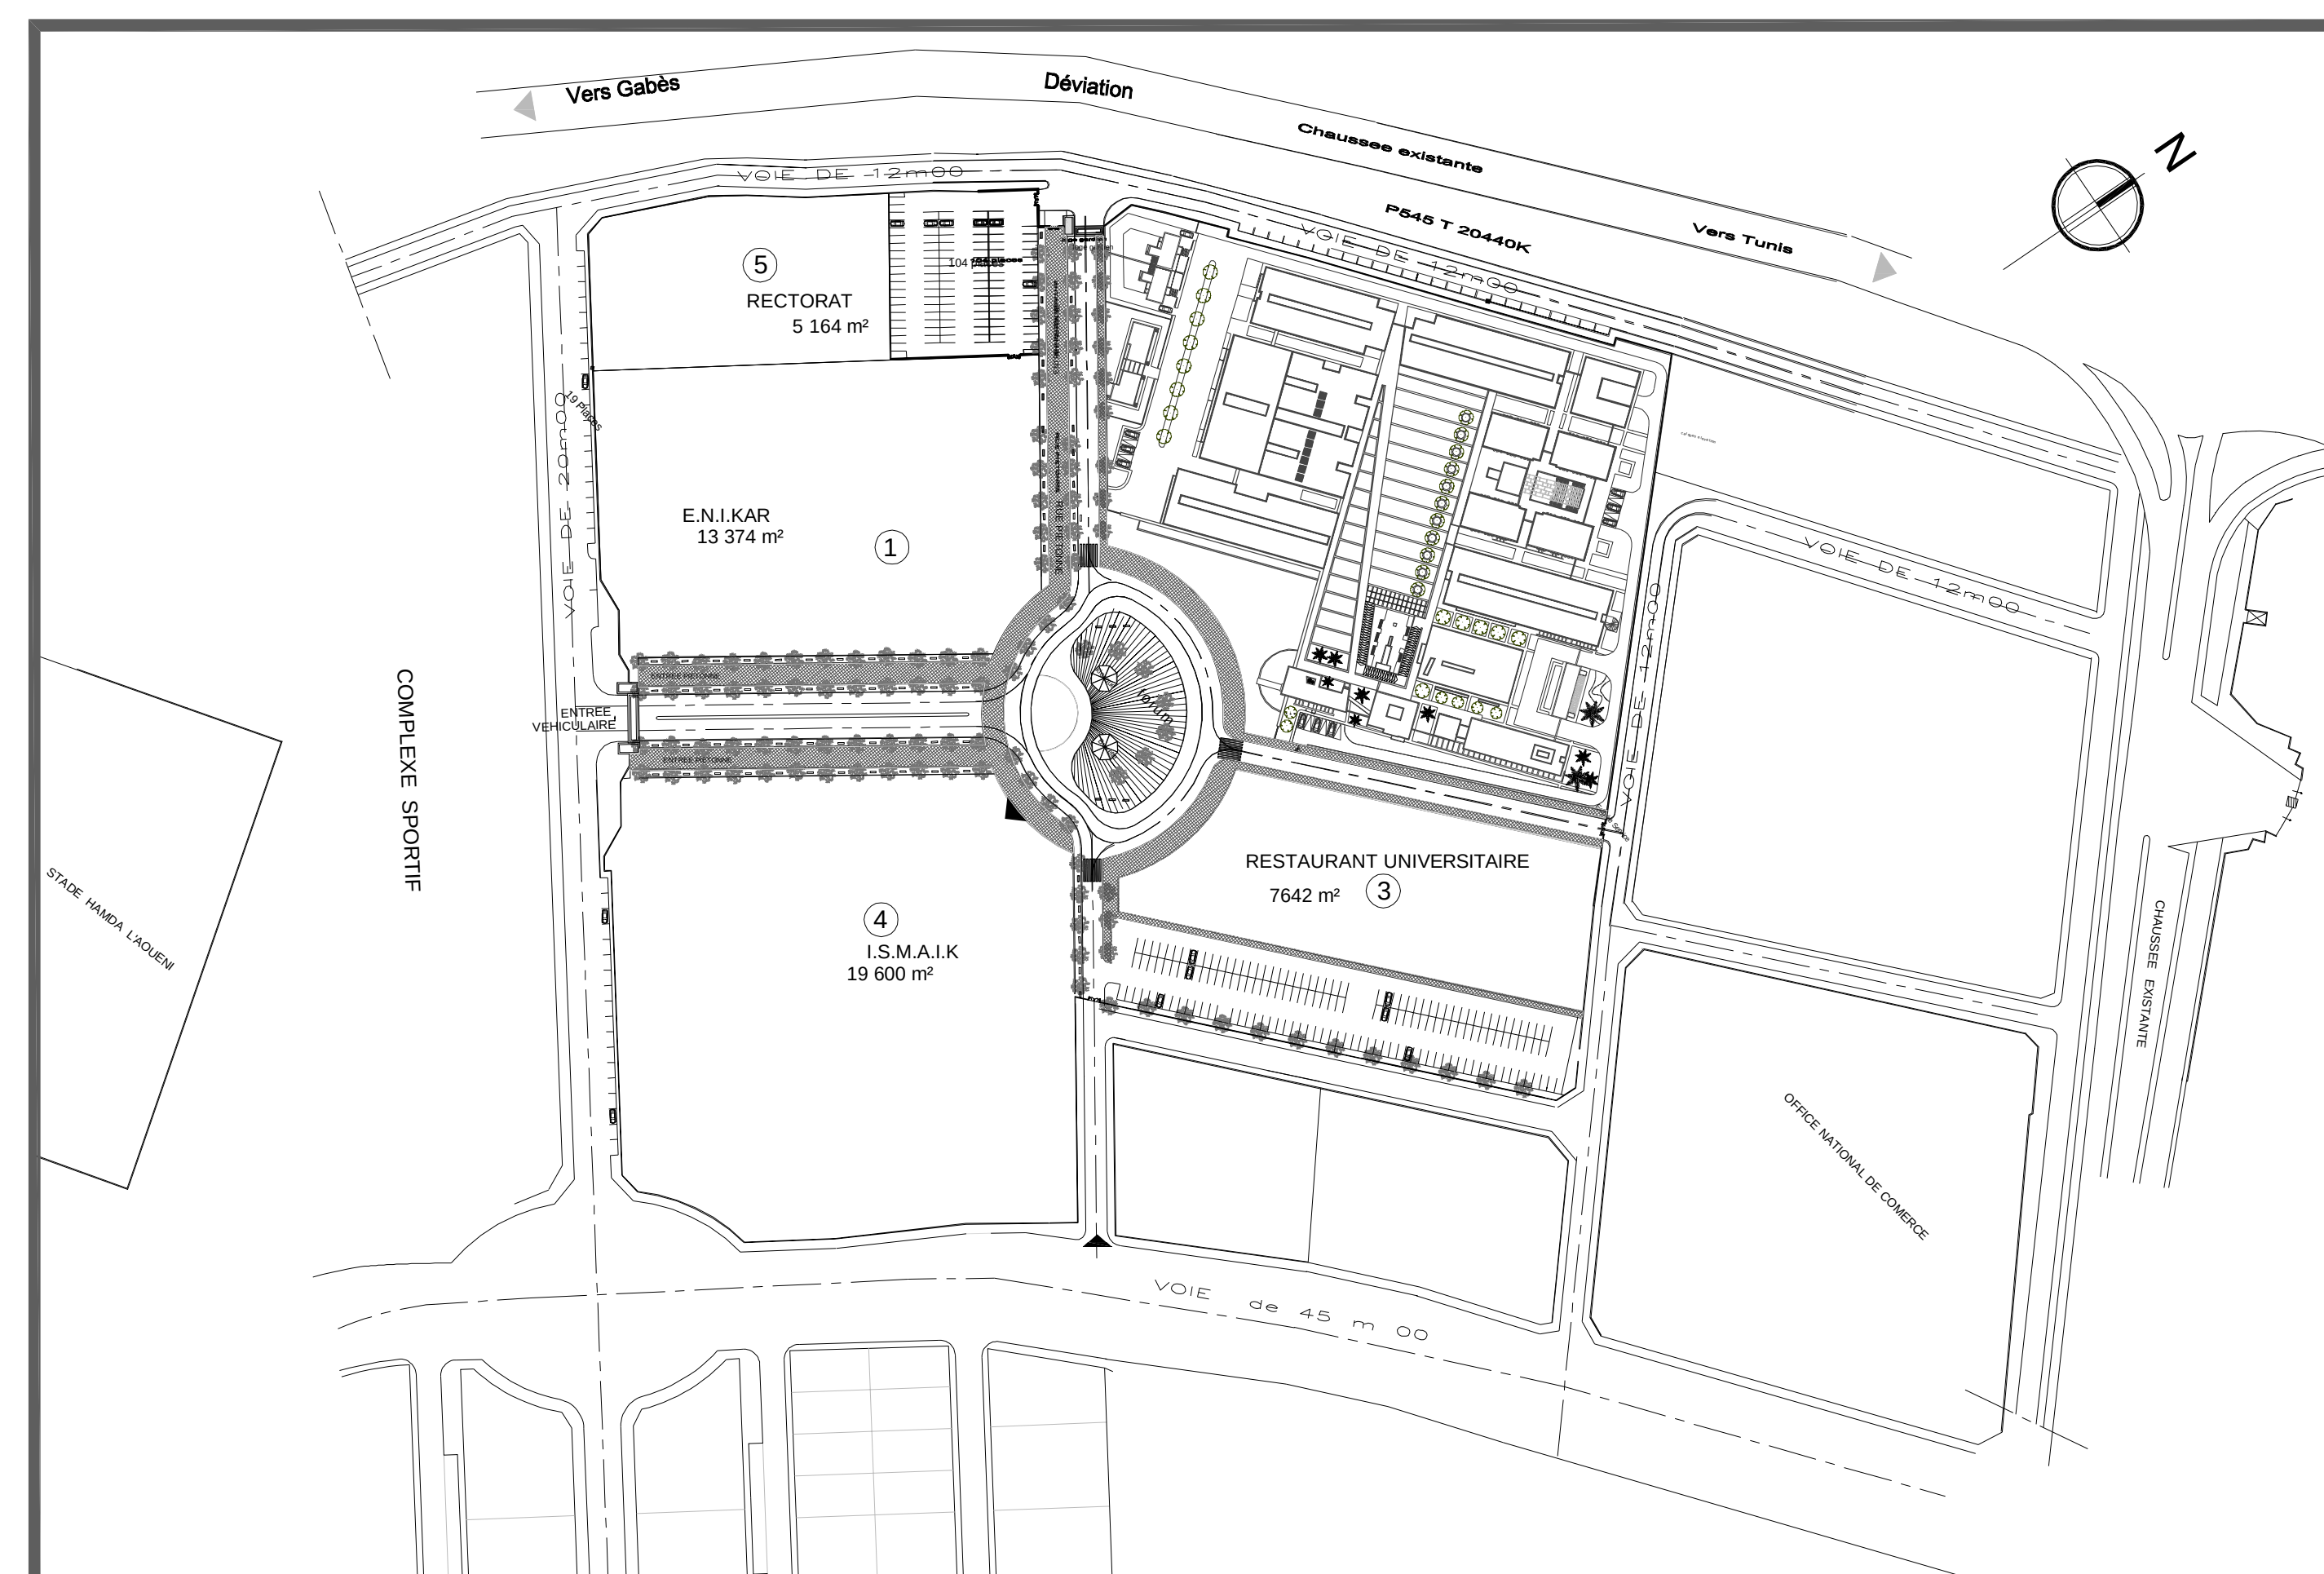


1ère Tranche  
2ème Tranche

PHASAGE DU PROJET

PLAN IMPLANTATION ech 1/2000

- A1. Direction
- A2. Secrétariat Général
- B. Département
- D. Bibliothèque
- E. Bloc Socio Culturel
- F. Services Généraux
- G. Locaux Techniques
- H. Logement de Fonction
- C1. Enseignement Commun
- C2. Département de Génie Civil
- C3. Département de Mathématique et d'Informatique
- C4. Département de Génie Mécanique
- C5. Département de Génie Industriel

EPANNELAGE FONCTIONNEL

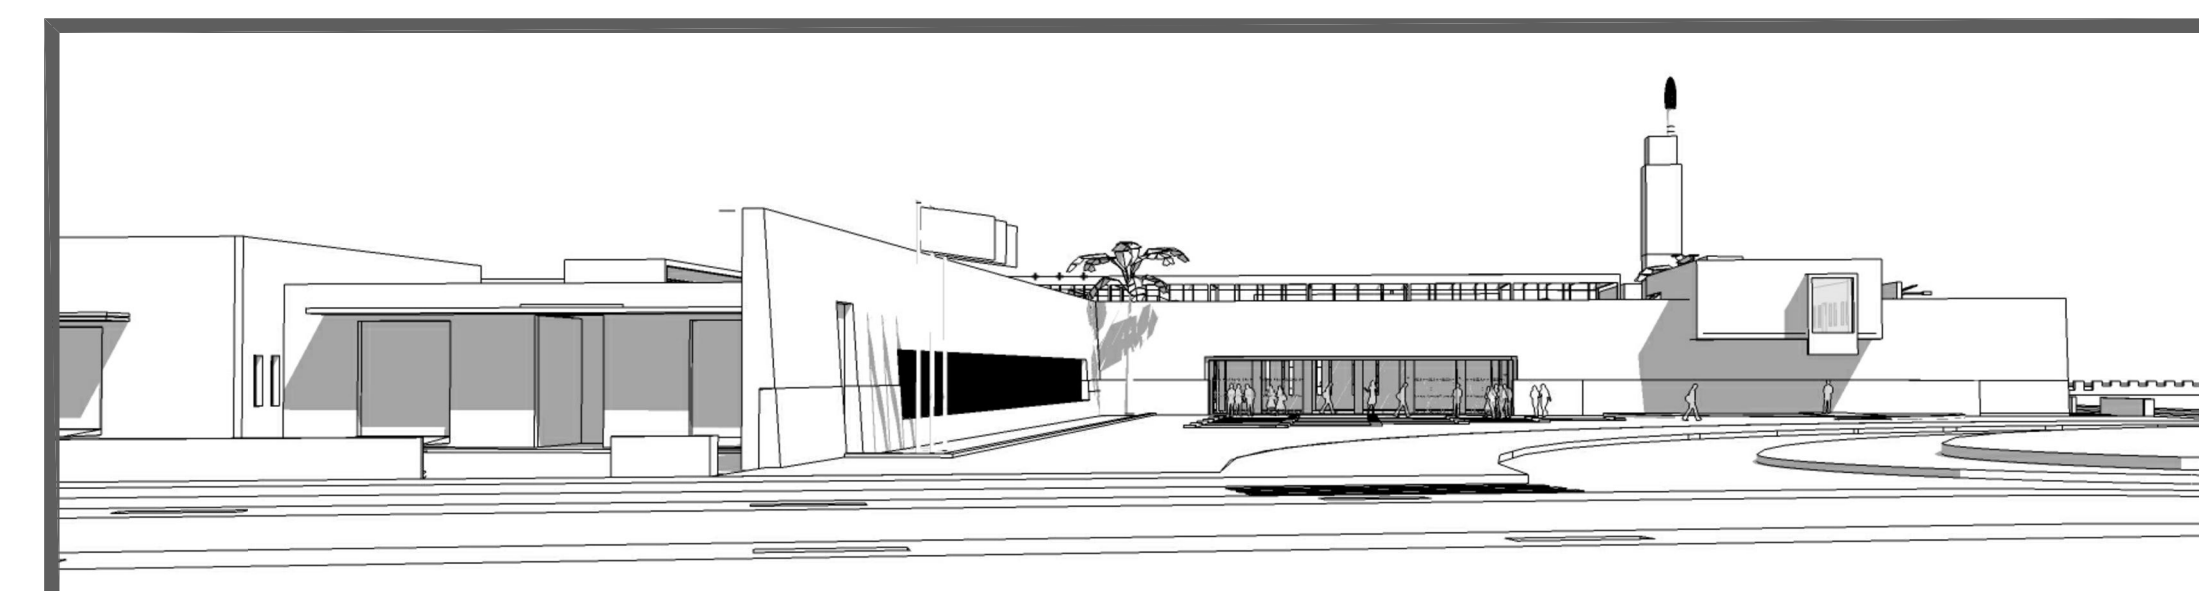

CONCOURS NATIONAL D'ARCHITECTURE A UN DEGRE  
PROJET DE CONSTRUCTION  
DE L'INSTITUT SUPERIEUR DES SCIENCES APPLIQUEES  
ET DE LA TECHNOLOGIE DE KAIROUAN

ARCHITECTE MANDATAIRE : Jalel SAKLI  
ARCHITECTE ASSOCIE : Anis BOUDEN  
ARCHITECTE ASSOCIE : Mohamed Ali BEN AFIA

Adresse: 27 bis, Avenue Fattouma Bourguiba, 2036, La Soukra