


PERSPECTIVE GENERALE

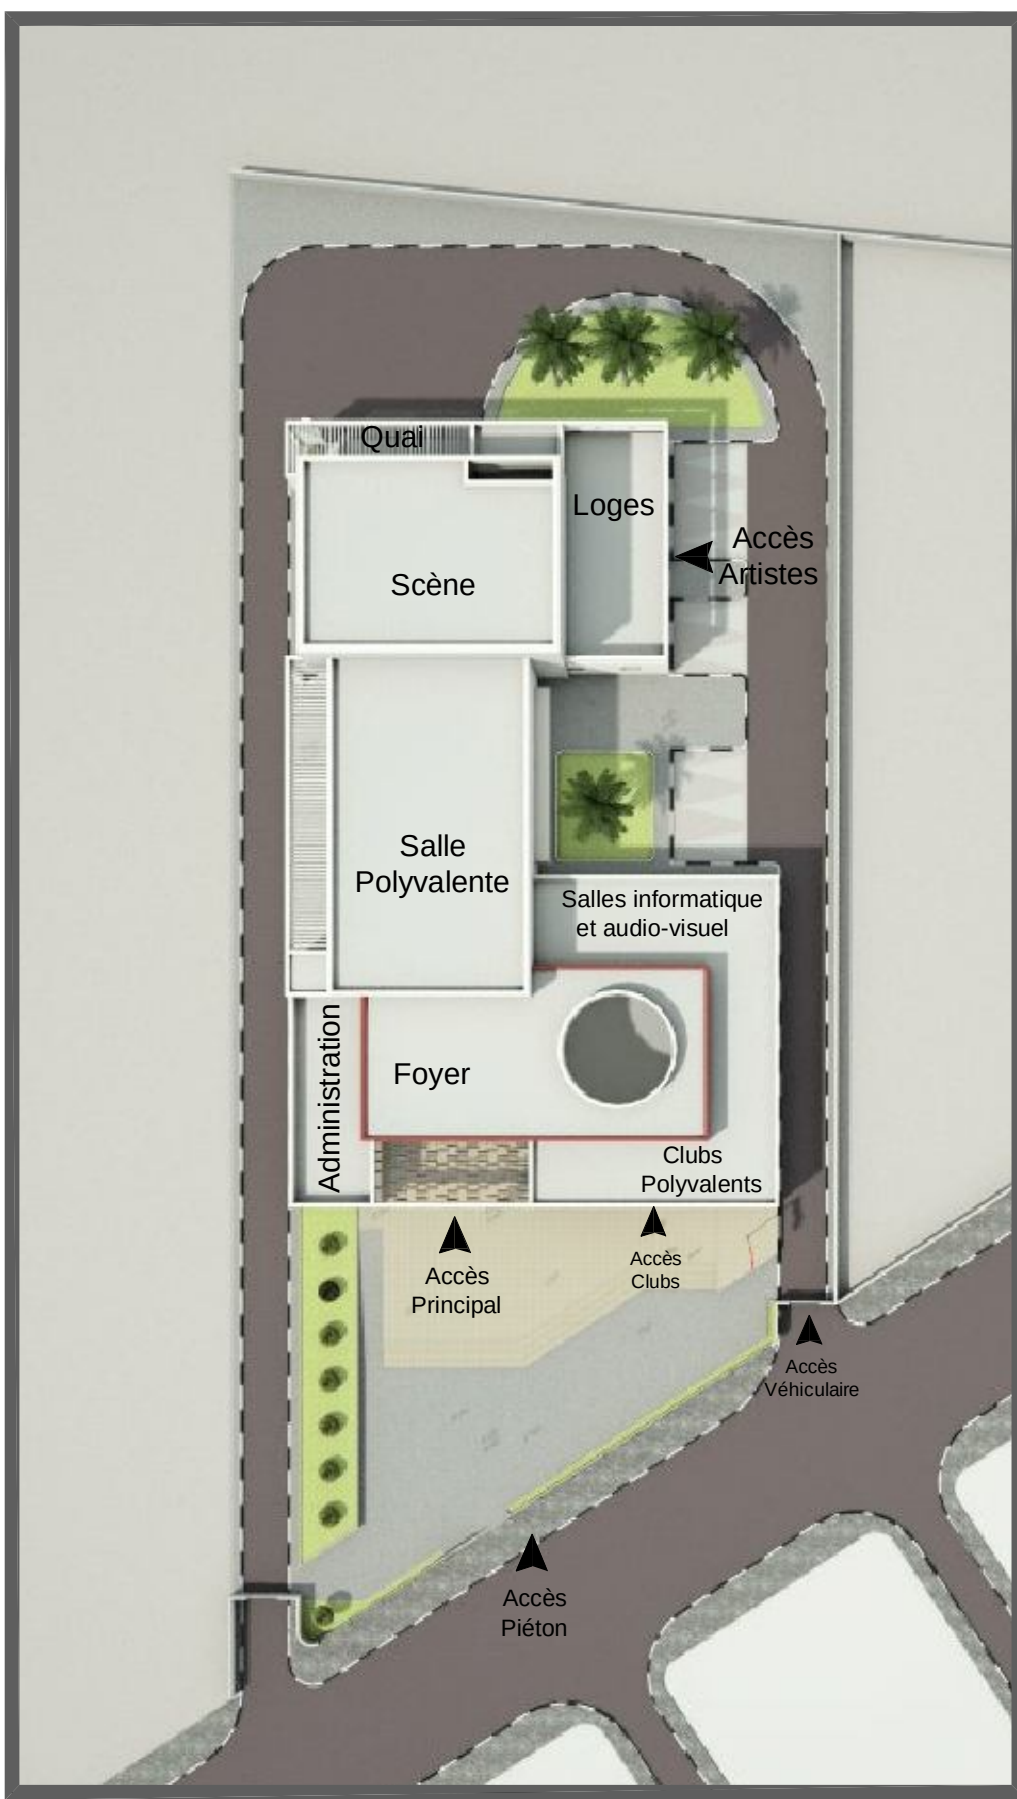

Si autrefois l'architecture des maisons de cultures était considérée dans une logique de lieux passifs, maintenant elle voit son champ s'élargir pour placer ses habitués dans une position d'accompagnement au cadre éducatif, d'expression personnelle, d'échange et de développement culturel.

De ce fait, on a cherché dans notre conception à dépasser le rôle principal de la maison de culture pour proposer un lieu de rencontre, de loisir, de détente et d'épanouissement à l'image de la jeunesse d'aujourd'hui.

Nous avons conçu donc un bâtiment sobre, élégant, majestueux, économique et ouvert sur la modernité tout en incluant des éléments architectoniques et d'ornementation inspirés du patrimoine Tunisien.

Un refuge ayant pour rôle la sécurité des usagers annonce le projet.

L'accès se fait sur un parvis menant de l'entrée qui se fait à travers un porche vers le foyer du projet, le foyer est ponctué d'un desk d'accueil et d'information, d'un hall d'expo et de réception, d'un coin buvette et d'un accès administration.

Les clubs se développent autour d'un patio de forme circulaire entouré par une galerie de circulation couverte ouverte.

En face de l'entrée se trouve la salle polyvalente de spectacle et à gauche l'administration.

L'aille pédagogique organisée autour d'un patio permet d'abriter des extensions pour les expositions du foyer.

Quant à la salle de spectacle, elle est accessible directement du hall d'accueil; ceci assure son autonomie si besoin y est. Le choix de sa masse, ses formes et de ses matériaux font d'elle un élément signalétique fort à l'extérieur et apportent un confort acoustique considérable à l'intérieur. En outre, des fentes latérales assurent l'aération et un éclairage indirect.

Finalement, par sa conception, ses formes, ses couleurs et ses espaces, ce projet apporte une réponse architecturale convenable qui met en valeur le rôle social, éducatif et culturel des maisons de culture.

PLAN MASSE



TABLEAU DES SURFACES UTILES		Projet	Prog.
I FOYER			
I.1	Hall + Accueil + Buvette	84.6	80
I.2	Bureau Directeur	17	15
I.3	Bureau Animateurs	15.1	15
I.4	Sanitaire	6.2	10
II SALLE POLYVALENTE DE SPECTACLES			
II.1	La Salle	250.6	210
II.2	La Scène	189.1	140
II.3	Loge de groupe 1	19.8	20
II.4	Loge de groupe 2	19.2	20
II.5	Loge individuelle 1	11.5	10
II.6	Loge individuelle 2	11.5	10
II.7	Dégagement	25.5	20
II.8	Cabines	19	25
II.9	Sanitaires	11.5	20
II.10	Sanitaires personnels	3.5	00
III SALLE D'ACTIVITE			
III.1	Club polyvalent 1	27.7	30
III.2	Club polyvalent 2	29.1	30
III.3	Club polyvalent 3	27.5	30
III.4	Club polyvalent 4	30.7	30
III.5	Salle Audio-visuel	30.9	35
III.5	Salle Informatique	30.9	35
III.6	WC	8.8	10

SURFACES HORS OEUVRE		
Total		1098 m²

ESTIMATION DES COUTS		
LOTS	Prix Unitaire	Prix Total
Génie Civil	670 DT/m²	735.660 DT
Electricité	100 DT/m²	109.800 DT
Climatisation et Plomberie sanitaire	200 DT/m²	219.600 DT
SOUS TOTAL		1 065.060 DT
Etudes et controle	10%	106.506 DT
TOTAL GENERAL		1 171.566 DT

COUT TOTAL	1 172.000 DT
------------	--------------



VUES SEQUENTIELLES

TABLEAU DES SURFACES

