


PROJET DE CONSTRUCTION D'UN RESTAURANT UNIVERSITAIRE "SABRA" AU COMPLEXE UNIVERSITAIRE RACCADA

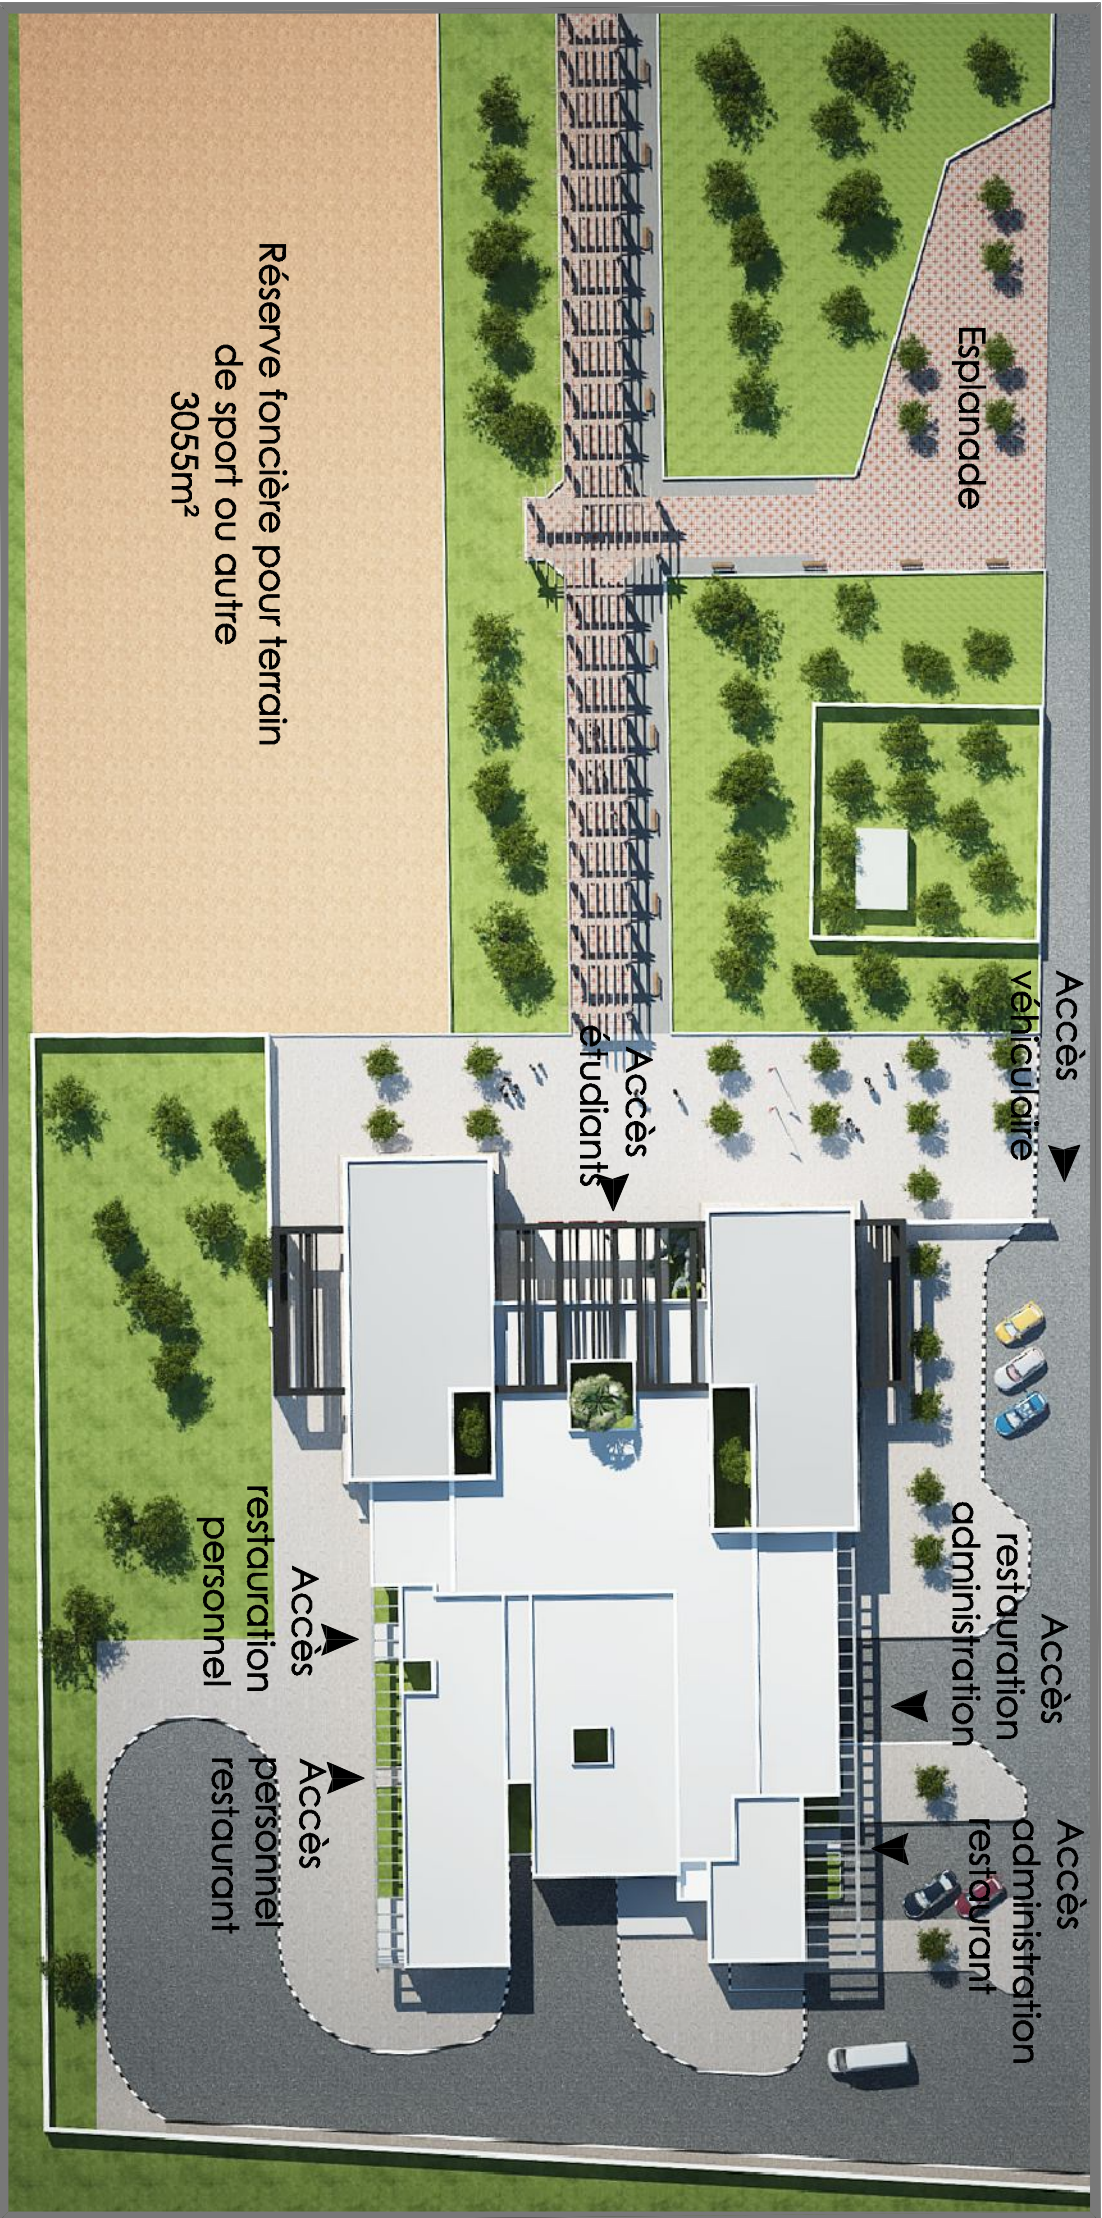

Nous avons conçu un bâtiment sobre élégant, mojestieux, économique et ouvert sur la modernité tout en incluant des éléments architectoniques et d'ornementation puisés dans le patrimoine de la ville de Kairouan .

nous avons donc utilisé les patios comme système d'éclairage et d'aération ainsi que la pierre emblème du bâtiment kairouanais au niveau des façades.

Le projet du futur restaurant universitaire est conçu de manière compacte et sur un seul niveau il est ainsi conforme au règlement d'urbanisme de la zone offrant une économie importante sur le lot fondation

et la surface des terrasses permettant une grande économie d'énergie. Ce choix a permis de dégager une grande réserve foncière pour une éventuelle extension.

Les accès du restaurant universitaire ont été gérés de manière hiérarchisés par rapport au flux des étudiants ainsi que les différentes voies desservant le lot.

Pour accentuer l'importance du forum central accès principal du projet nous avons crée un parcours qui commence par une grande esplanade de rassemblement et un large parvis visant également à fluidifier et à gérer le va et vient des étudiants aux heures de pointes.

L'organisation fonctionnel du projet se veut très rigoureuse et concise par rapport à la complexité qui peut être générée par les différents circuits du programme qui ne sont pas compatibles.



PLAN MASSE ech 1/ 500

PERSPECTIVE GENERALE



VUES 3D

TABLEAU DES SURFACES			Programme	Projet
A	RESTAURATION			60
A.1	Hol d'entrée, réception, guichet, contrôle.		36	60
A.2.1	Bloc sanitaires entrées.		10	10,3
A.2.2	Bloc sanitaires entrées.		10	10,3
A.3.1	Hol de sortie.		20	13
A.3.2	Hol de sortie.		20	13
A.4.1	Bloc sanitaires sortie.		12	19,7
A.4.2	Bloc sanitaires sortie.		12	19,7
A.5.1	Salle de restauration pour étudiants		250	259,9
A.5.2	Salle de restauration pour enseignants 80 places		250	276,2
A.6	Salle de restauration pour personnel du campus		100	92
A.7	Salon d'accueil		20	25
A.8	Salle de restauration pour personnel du campus		60	60
B	CUISINE			
B.1	Bloc cuisson + boxes de réception		200	220
B.2.1	Chambre froide		9	8,5
B.2.2	Chambre froide		9	8,8
B.2.3	Chambre froide		9	8,8
B.3	Local armoires frigorifiques		24	24,3
B.4	Dépot légumes		20	32
B.5	Dépot produits alimentaires		30	28
B.6	Dépot pain		9	7
B.7	Dépot vaisselle		20	23,9
B.8	Laverie		25	19,6
B.9.1	Plonge retour plateaux		30	30,3
B.9.2	Plonge retour plateaux		30	31,5
B.10.1	Local poubelle instantanée		3	6,2
B.10.2	Local poubelle instantanée		3	6,2
B.11	Dépot produits de nettoyage		3	3,5
B.12	Local poubelle		9	3
B.1.3	Bureau chef de cuisine		9	9
B.1.4	Bureau hygiène		9	8,6
B.1.5	Bureau magasinier		9	8,6
C	LOCAUX ADMINISTRATIFS			
C.1	Bureau directeur		16	17
C.2	Bureau économie		14	14,9
C.3.1	Bureau agent		12	12
C.3.2	Bureau agent		12	12
C.4.1	Bloc sanitaires		3	5,2
C.4.2	Bloc sanitaires		3	5,2
D	LOCAUX DE SERVICES			
D.1.1	Vestibules ouvriers-douches-sanitaires		24	23,3
D.1.2	Vestibules ouvriers-douches-sanitaires		24	23,3
D.2	Bucanderie		12	13
D.3	Atelier entretien et maintenance		20	21
D.4	Megasin		30	29
D.5	Loge gardien-sanitaires		9	9
E	LOCAUX TECHNIQUES			
E.1	Local générateur d'eau chaude		12	12,2
E.2	Poste transformateur		30	31,5
E.3	Groupe électrogène		20	21

RECAPITULATIF			
SURFACE TOTALE DU PROGRAMME PROPOSE			2009.00 m²
SURFACE TOTALE DU PROGRAMME DE NOTRE PROJET			2013.40 m²
Désignation	Surface m²	Prix m²	Total DT
1- Génie Civil + lots spéciaux	2013,40	920,000	1 852 928,000
2- VMD & Aménagements divers	2013,40	25,000	50 335,000
3- Equipement de cuisine		Ferfait	350 000,000
TOTAL (coût travaux)			2 252 663,000
Taux de tolérance			112 633,150
TOTAL 2			2 365 296,150
Honoraires d'études et contrôle technique			164 879, 000
TOTAL 3			2 530 125,150
Divers branchements + Imprévus			75 300,000
TOTAL GENERAL (T.T.C.)			2 605 425,150

