

PERSPECTIVE GENERALE



PLAN MASSE ech 1/500

Si autrefois l'architecture des maisons de cultures était considérée dans une logique de lieux passifs, maintenant elle voit son champ s'élargir pour placer ses habitués dans une position d'accompagnement au cadre éducatif, d'expression personnelle, d'échange et de développement culturel.

De ce fait, on a cherché dans notre conception à dépasser le rôle principale de la maison de culture pour proposer un lieu de rencontre, de loisir, de détente et d'épanouissement à l'image de la jeunesse de Sidi Bouzid d'aujourd'hui.

Nous avons conçu donc un bâtiment sobre, élégant, majestueux, économique et ouvert sur la modernité tout en incluant des éléments architectoniques et d'ornementation inspirés du patrimoine Tunisien.

Un refuge ayant pour rôle la sécurité des usagers longe l'axe du lycée voisin, annonce le projet.

L'accès se fait sur un parvis menant de l'entrée qui se fait à travers un porche vers le foyer du projet (Fig.1), le foyer est ponctué d'un desk d'accueil et d'information, d'un hall d'expo et de réception, d'un coin buvette et d'un accès administration.

Le projet se développe autour d'un patio central de forme carré entouré par une galerie de circulation couverte ouverte (Fig.2), à droite l'aile pédagogique, à gauche la salle polyvalente de spectacle et au fond les salles informatiques et audiovisuel.

Les galeries de circulations sont ponctués par des portiques et des brises soleil qui assurent une ventilation naturelle pouvant être le support du circuit de la climatisation centrale (Fig.3).

L'aile pédagogique est organisé autour d'un autre patio, plus intime et pouvant abriter les petites activités extérieures .

Quant à la salle de spectacle, elle est accessible soit du patio central, soit du hall d'accueil; ceci assure son autonomie si besoin y est. Le choix de sa masse, ses formes et de ses matériaux font d'elle un élément signalétique fort à l'extérieur et apportent un confort acoustique considérable à l'intérieur. En outre, des fentes latérales assurent l'aération et un éclairage indirect (Fig.4).

Finalement, par sa conception, ses formes, ses couleurs et ses espaces, ce projet apporte une réponse architecturale convenable qui met en valeur le rôle social, éducatif et culturel des maisons de culture.



Figure 1



Figure 2



Figure 3



Figure 4

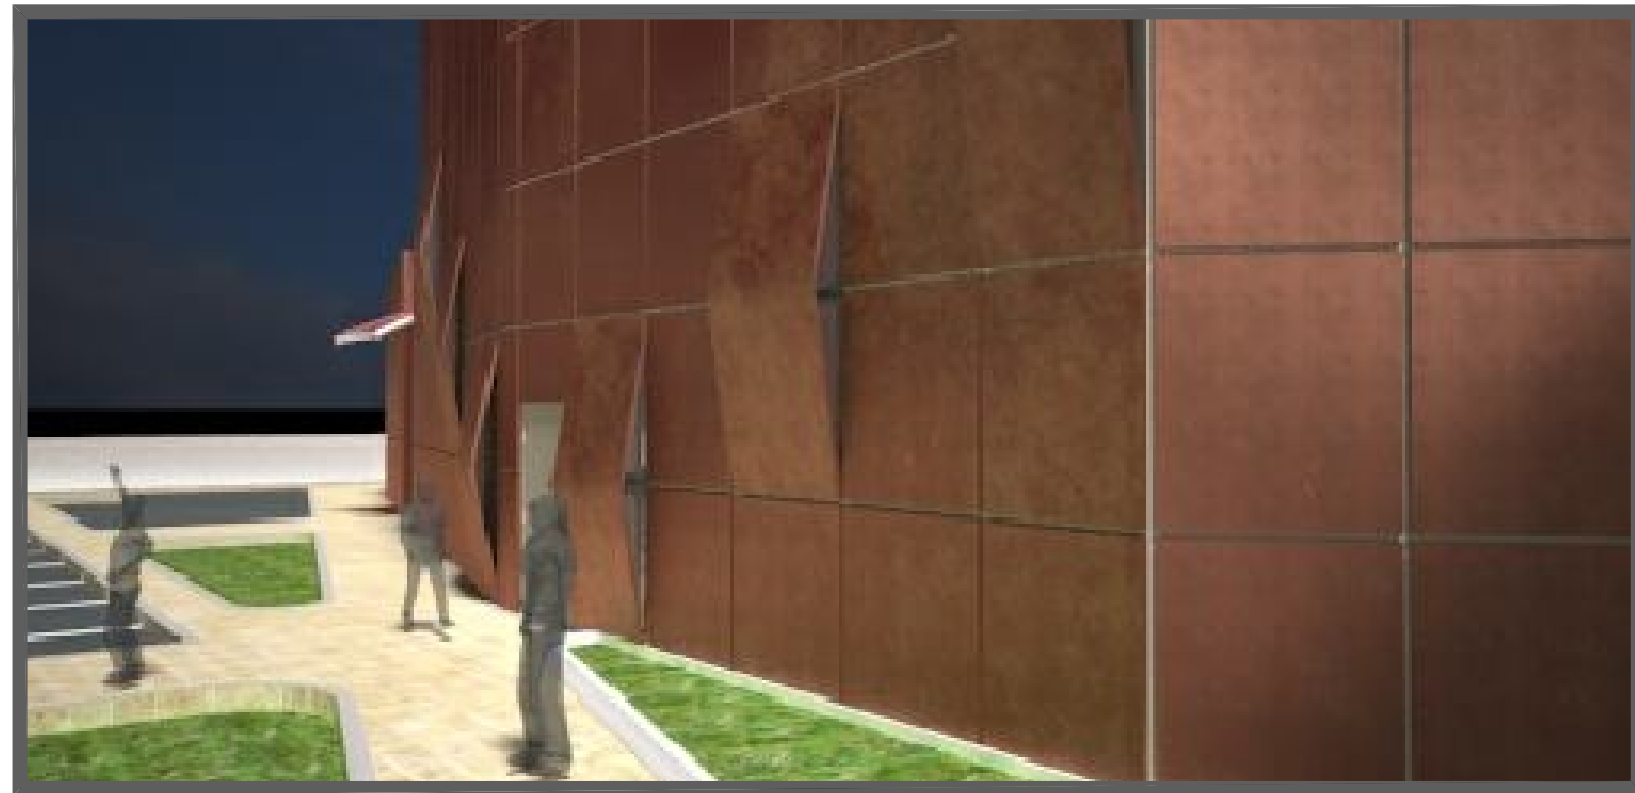


Figure 4

TABLEAU DES SURFACES UTILES		
I	FOYER	C
I.1	Hall + Accueil + Buvette	75.1
I.2	Bureau Directeur	17
I.3	Bureau Animateur	15
I.4	WC Administration	9.7
II	SALLE POLYVALENTE DE SPECTACLES	
II.1	La Salle	226.5
II.2	La Scène	133.9
II.3	Loge de groupe 1	19.8
II.4	Loge de groupe 2	17.9
II.5	Loge individuelle 1	13
II.6	Loge individuelle 2	12.5
II.7	Dégagement	34.3
II.8	Régie Latérale 1	10.3
II.9	Régie Latérale 2	21.7
II.10	WC	13.7
III	SALLE D'ACTIVITE	
III.1	Club polyvalent 1	35.1
III.2	Club polyvalent 2	30.6
III.3	Club polyvalent 3	30.6
III.4	Club polyvalent 4	35.1
III.5	Salle Audio-visuel	34.7
III.5	Salle Informatique	34.7
III.6	WC	8.5

SURFACES HORS OEUVRE	
Total	1146.7 m² *

ESTIMATION DES COUTS		
LOTS	Prix Unitaire	Prix Total
Génie Civil	650 DT/m²	745.355 DT
Electricité	100 DT/m²	114.670 DT
Climatisation et Plomberie sanitaire	200 DT/m²	229.340 DT
VRD	25 DT/m²	28.667 DT
Sous Total		1 118.032 DT
Etudes et controle	10%	111.803 DT
TOTAL GENERAL		1 229.835 DT

COUT TOTAL	1 230.000 DT
------------	--------------